
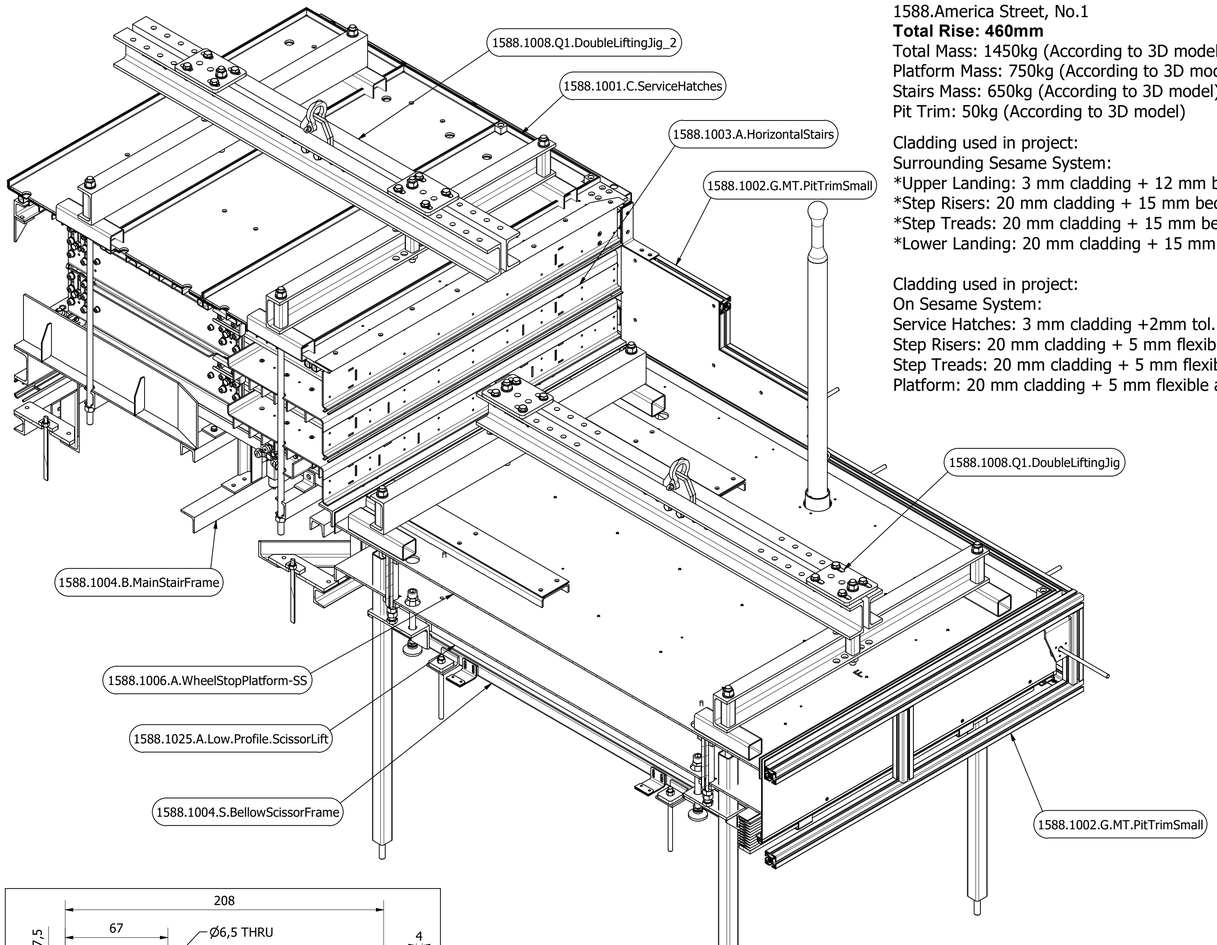


1588.America Street, No.1
Total Rise: 460mm
Total Mass: 1450kg (According to 3D model)
Platform Mass: 750kg (According to 3D model)
Stairs Mass: 650kg (According to 3D model)
Pit Trim: 50kg (According to 3D model)


Cladding used in project:
Surrounding Sesame System:
*Upper Landing: 3 mm cladding + 12 mm bedding
*Step Risers: 20 mm cladding + 15 mm bedding
*Step Treads: 20 mm cladding + 15 mm bedding
*Lower Landing: 20 mm cladding + 15 mm bedding

Cladding used in project:
On Sesame System:
Service Hatches: 3 mm cladding +2mm tol. + 12 mm Cement Board
Step Risers: 20 mm cladding + 5 mm flexible adhesive + 18 mm Cement Board
Step Treads: 20 mm cladding + 5 mm flexible adhesive + 10 mm Cement Board
Platform: 20 mm cladding + 5 mm flexible adhesive + 10mm Cement Board


1588.1003.A.HorizontalStairs (1 : 10)

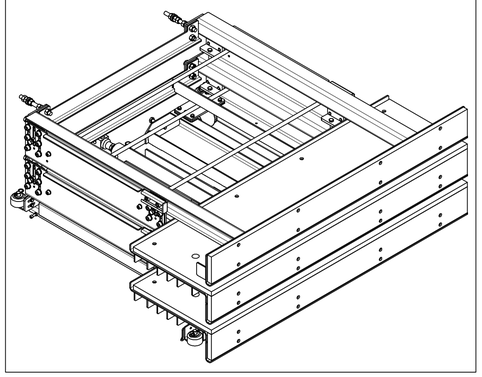


1588.1004.S.BellowScissorFrame (1 : 10)

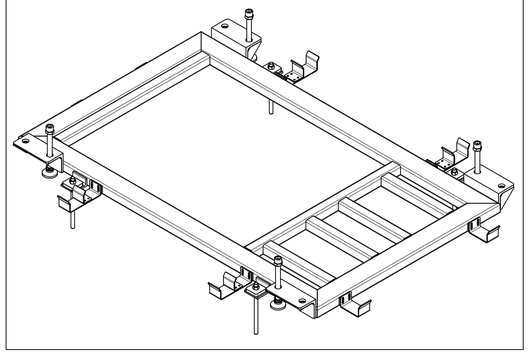


1588.1004.B.MainStairFrame (1 : 10)

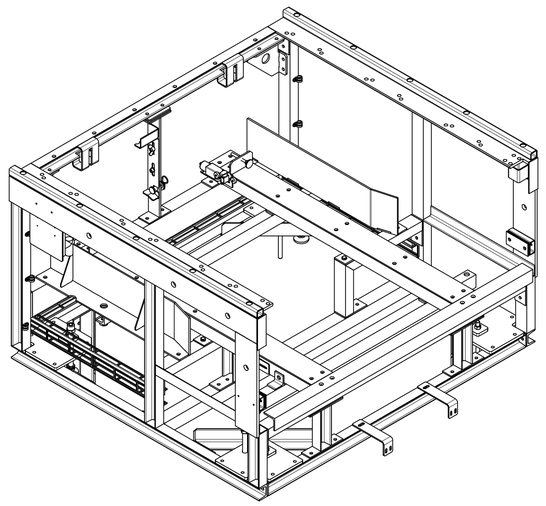


1588.1006.A.WheelStopPlatform-SS
(1 : 10)

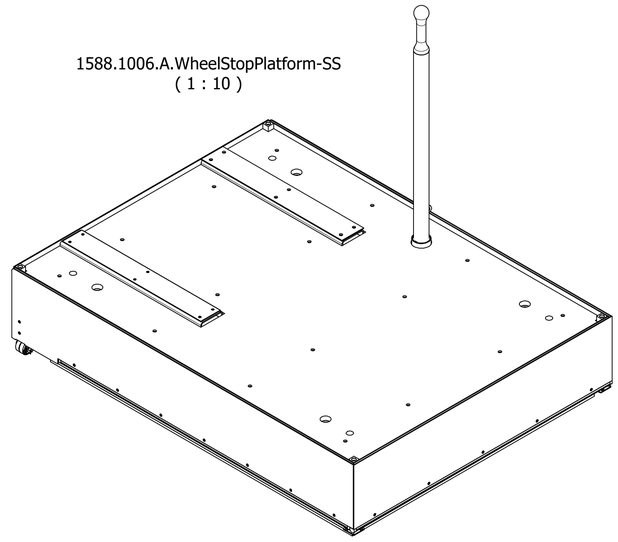


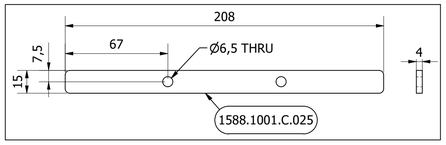


1588.1008.Q1.DoubleLiftingJig_2 (1 : 10)

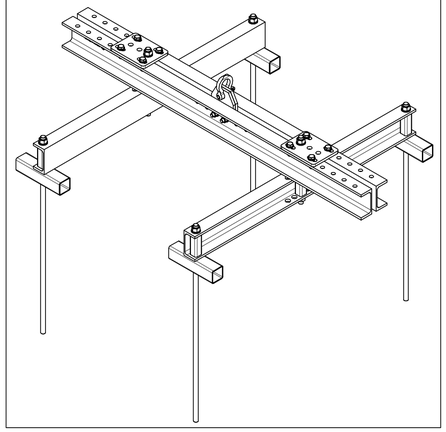


1588.1025.A.Low.Profile.ScissorLift (1 : 10)

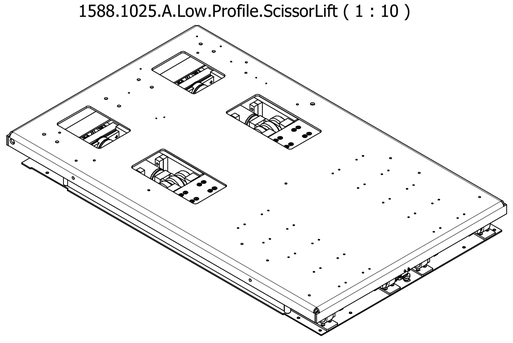


1588.1008.Q1.DoubleLiftingJig (1 : 10)

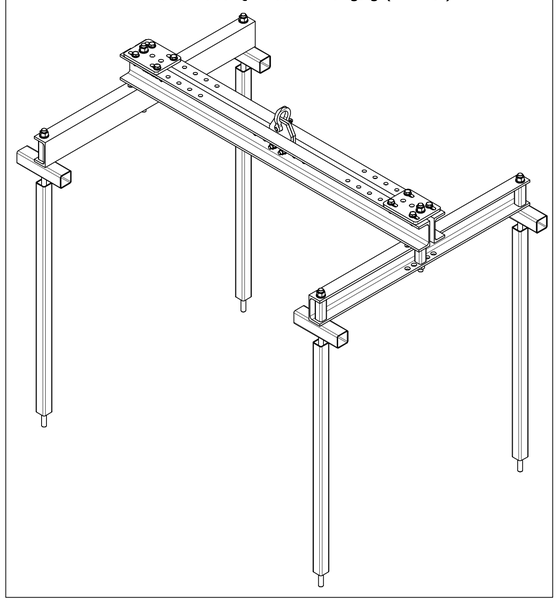

1588.1002.G.MT.PitTrimSmall (1 : 10)

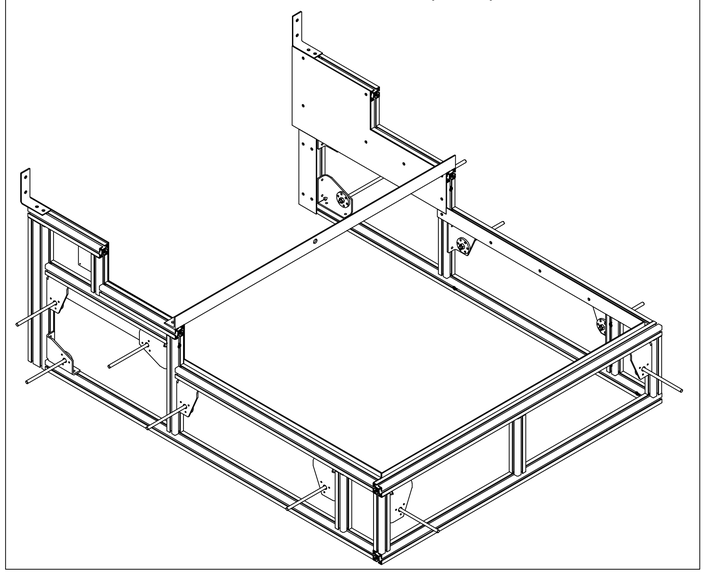

1588.1001.C.ServiceHatches (1 : 10)

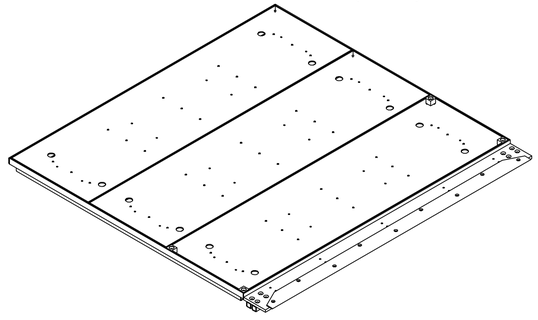


PARTS LIST					
ITM	QTY	PART NUMBER	DESCRIPTION	MATERIAL	VENDOR
1	4	1588.1001.C.024	Support	Stainless Steel	Laser Cut
2	2	1588.1001.C.025	Support	Stainless Steel	Laser Cut
3	1	1588.1001.C.ServiceHatches	Service hatch		Sesame
4	1	1588.1002.G.MT.PitTrimSmall	Pit trim		Sesame
5	1	1588.1003.A.HorizontalStairs	Main Assembly		Sesame
6	1	1588.1004.B.MainStairFrame	Stair frame		Sesame
7	1	1588.1004.S.BellowScissorFrame	SL Frame		Sesame
8	1	1588.1006.A.WheelStopPlatform-SS	Platform		Sesame
9	1	1588.1008.Q1.DoubleLiftingJig	Four points lifting jig		Sesame
10	1	1588.1008.Q1.DoubleLiftingJig_2	Four points lifting jig		Sesame
11	1	1588.1025.A.Low.Profile.ScissorLift	Scissor lift		Sesame


This drawing and the information it contains is the property of Sesame Access Systems LTD. and must not be copied or issued to any third party


Drawn by: IDSPC7
Checked by: S.J.Lyons
Date: 14/07/2026

Sesame ACCESS FOR ALL
Unit 1, Cumberland Works
Wintersell Business Park
Surrey, KT14 7LF
Tel: +44 (0)1784 440088
Fax:+44 (0)870 7053252
Email:forall@sesameaccess.com
Web:www.sesameaccess.com


Project name: 1588.America Street, No.1
Drawing pack: 1588.America Street, No.1_EngineeringDrawing.dwg
Process type: A (C - cutting, W - Welding, A - Assembly)
Revision: 0
Sheet: 1 / 12

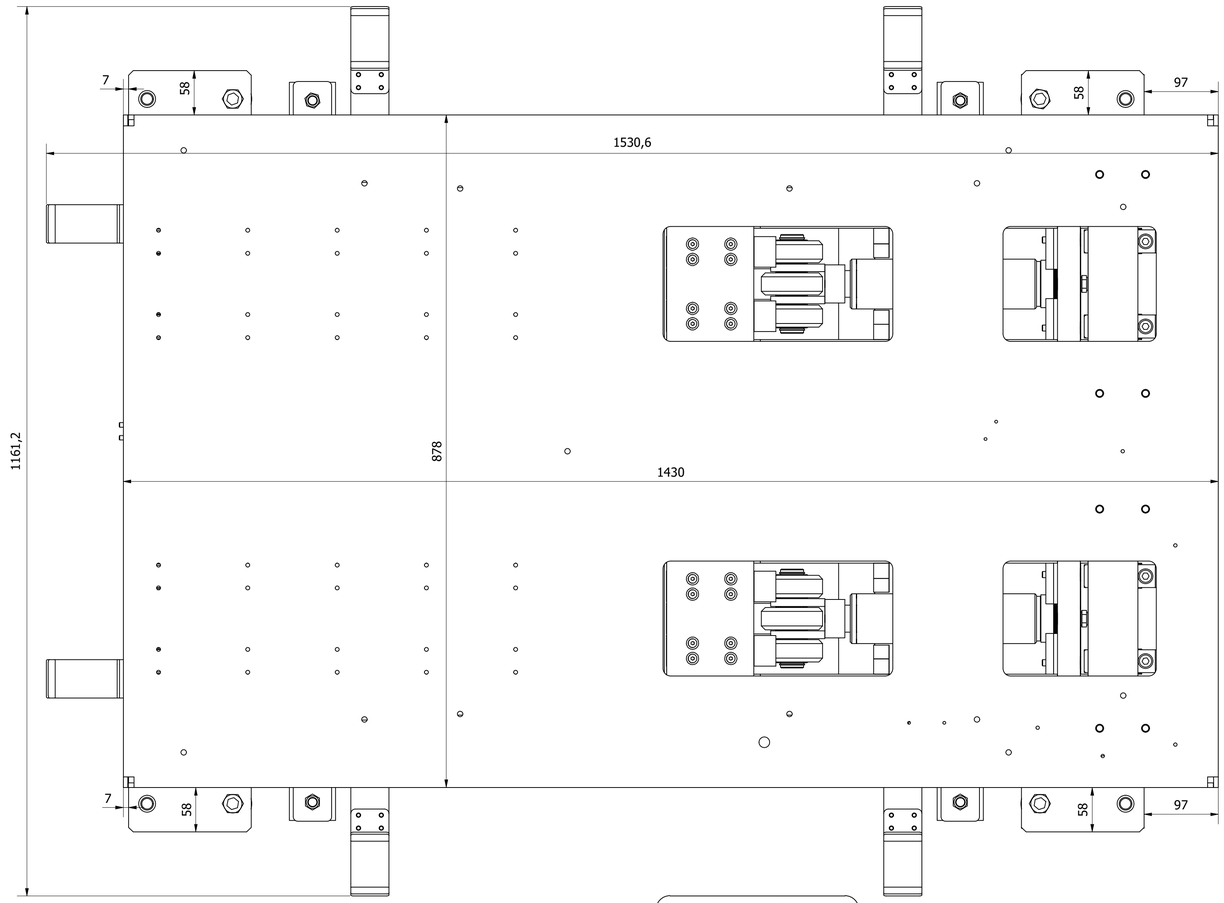

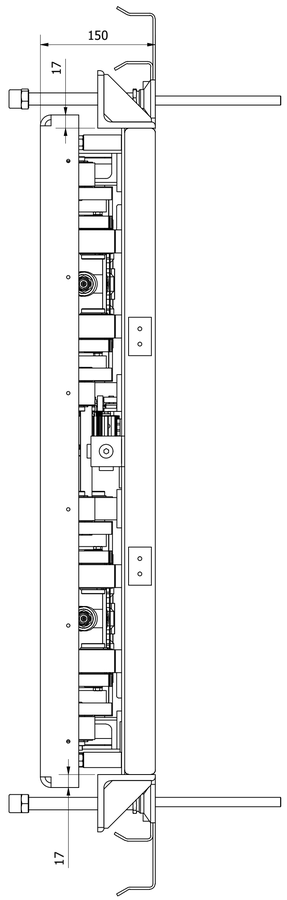


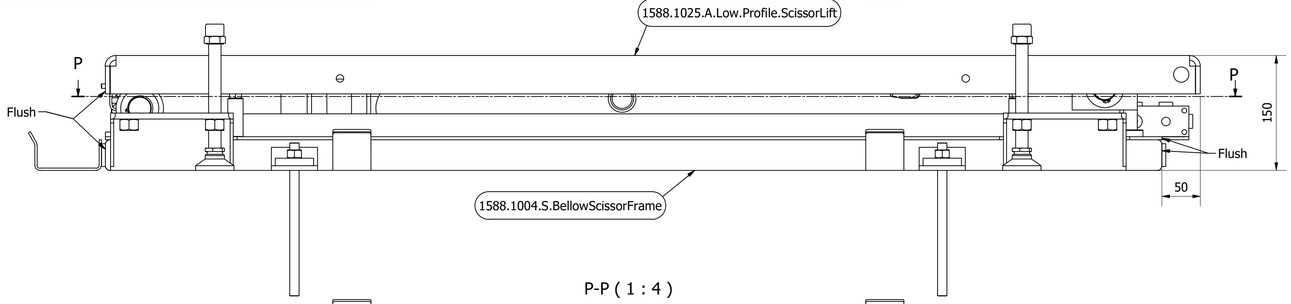


P-P (1 : 4)

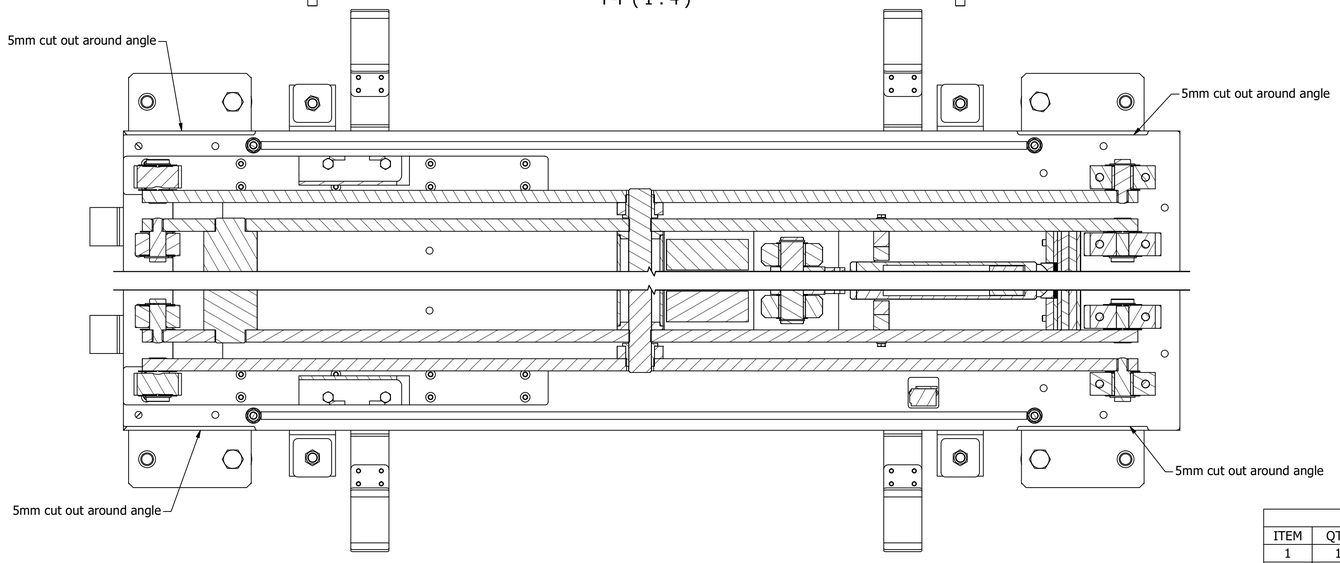

1588.1004.S.BellowScissorFrame (1 : 10)

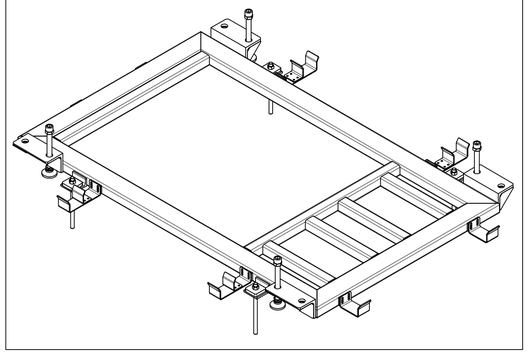

1588.1025.A.Low.Profile.ScissorLift (1 : 10)

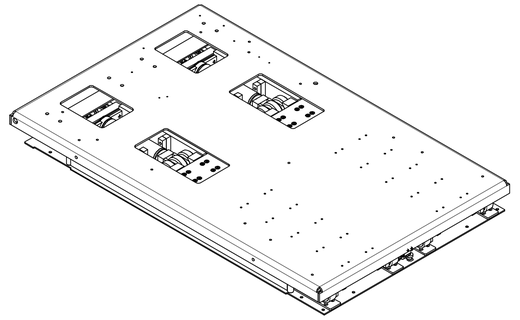

1588.America Street, No.1
Stage 1 Platform Assembly
Required parts on the right side

PARTS LIST					
ITEM	QTY	PART NUMBER	DESCRIPTION	MATERIAL	VENDOR
1	1	1588.1004.S.BellowScissorFrame	SL Frame		Sesame
2	1	1588.1025.A.Low.Profile.ScissorLift	Scissor lift		Sesame

Parts for:
1588.America Street, No.1
Stage 1 Platform Assembly


PARTS LIST					
ITEM	QTY	PART NUMBER	DESCRIPTION	MATERIAL	VENDOR
1	1	1588.1004.S.BellowScissorFrame	SL Frame		Sesame
2	1	1588.1025.A.Low.Profile.ScissorLift	Scissor lift		Sesame

This drawing and the information it contains is the property of Sesame Access Systems LTD. and must not be copied or issued to any third party


Drawn by: IDSPC7
Checked by: S.J.Lyons
Date: 14/07/2026

Sesame ACCESS FOR ALL
Unit 1, Cumberland Works
Wintersett Business Park
Surrey, KT14 7LF
Tel: +44 (0)1784 440088
Fax:+44 (0)870 7053252
Email:forall@sesameaccess.com
Web:www.sesameaccess.com


Project name: 1588.America Street, No.1
Drawing pack: 1588.America Street, No.1_EngineeringDrawing.dwg
Process type: C - cutting W - Welding A - Assembly
Revision: 0
Sheet: 2 / 12

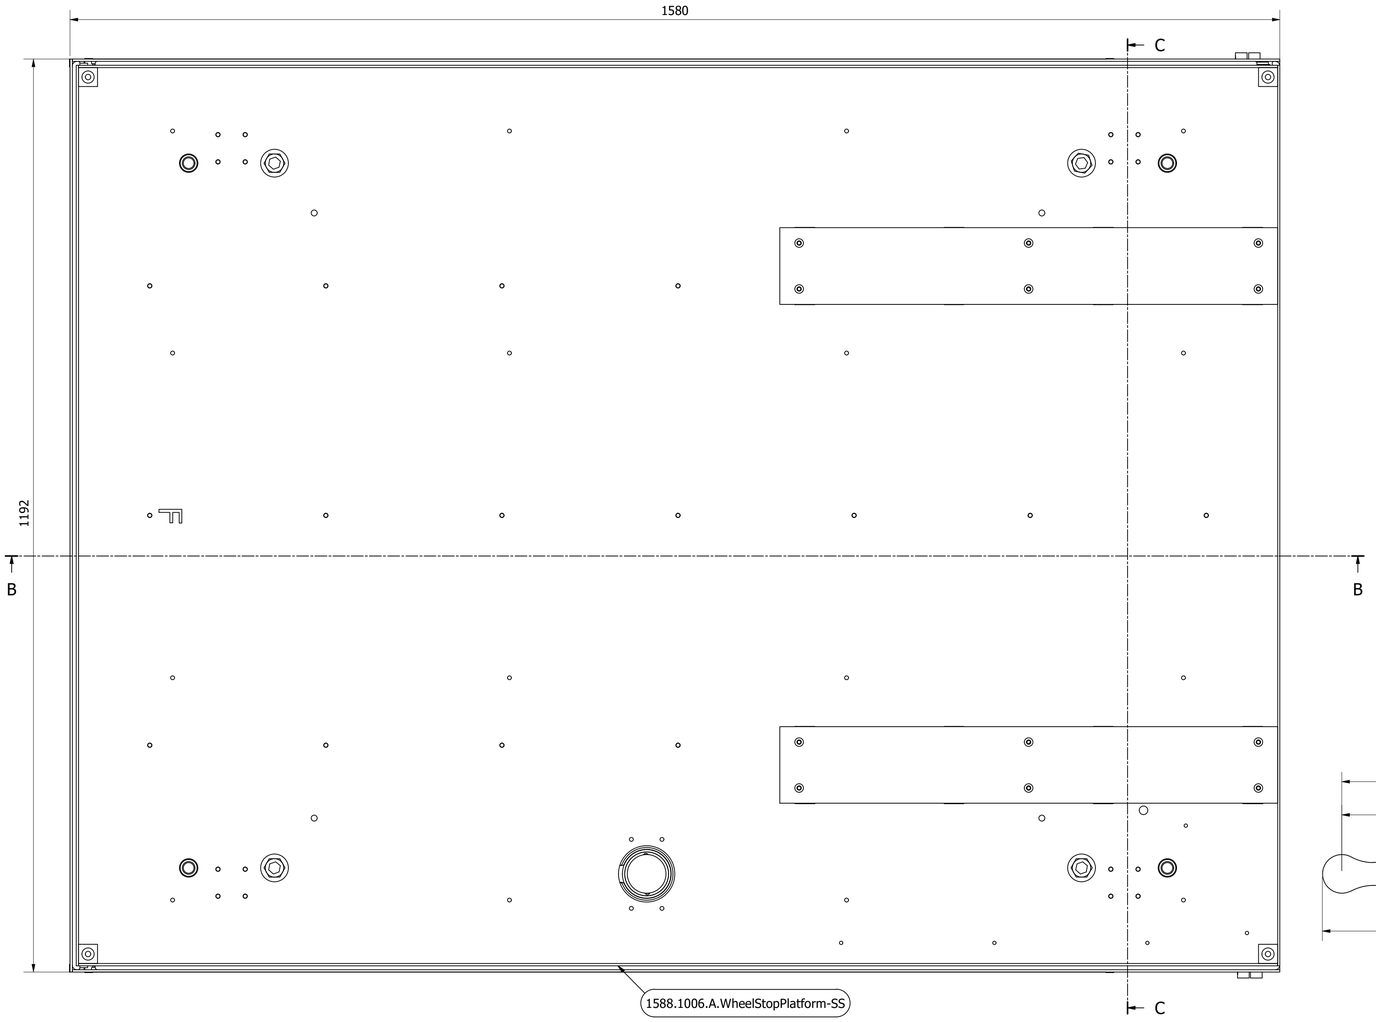


C-C (1 : 4)

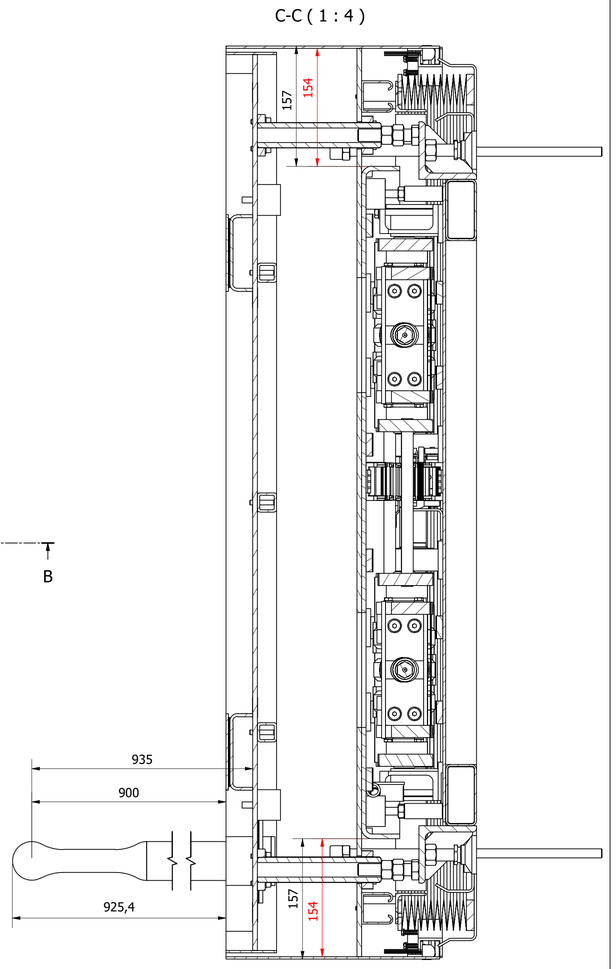


1588.1006.A.WheelStopPlatform-SS
(1 : 11)

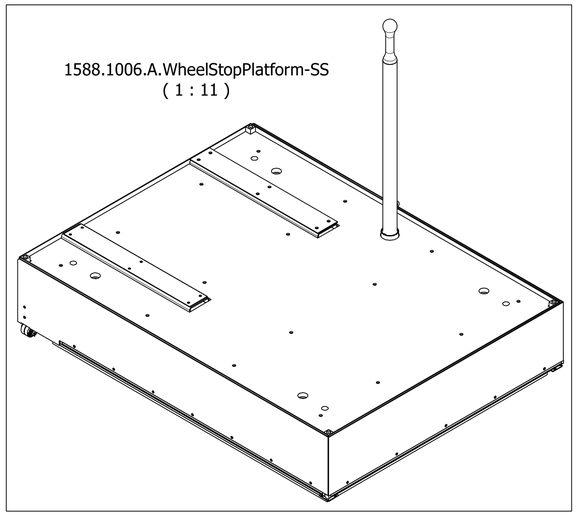

1588.America Street, No.1 (1 : 10)
Stage 1

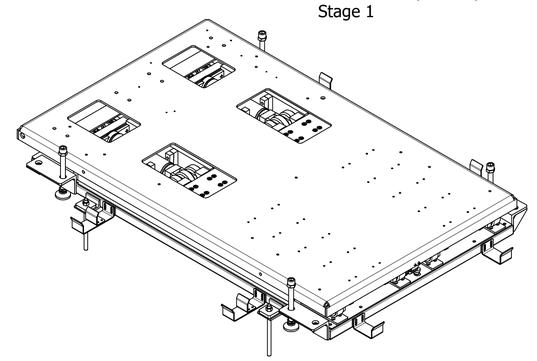

B-B (1 : 4)

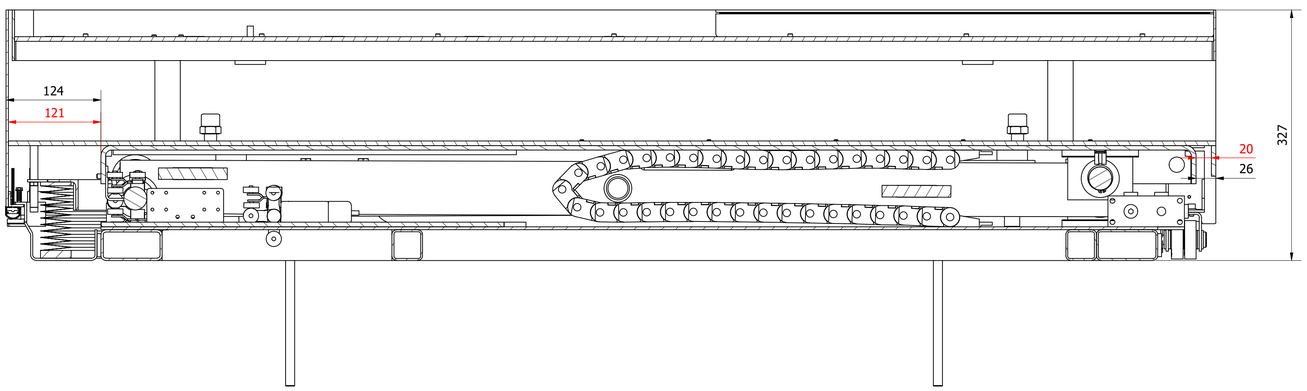

1588.America Street, No.1
Stage 2 Platform Assembly
Required parts on the right side

PARTS LIST					
ITEM	QTY	PART NUMBER	DESCRIPTION	MATERIAL	VENDOR
1	1	1588.1006.A.WheelStopPlatform-SS	Platform		Sesame
2	1	1588.America Street, No. 1	Stage 1		Sesame

Parts for:
1588.America Street, No.1
Stage 2 Platform Assembly

PARTS LIST					
ITEM	QTY	PART NUMBER	DESCRIPTION	MATERIAL	VENDOR
1	1	1588.1006.A.WheelStopPlatform-SS	Platform		Sesame
2	1	1588.America Street, No. 1	Stage 1		Sesame

This drawing and the information it contains is the property of Sesame Access Systems LTD. and must not be copied or issued to any third party


Drawn by: IDSPC7
Checked by: S.J.Lyons
Date: 14/07/2026

Sesame ACCESS FOR ALL
Unit 1, Cumberland Works
Wintersell Business Park
Surrey, KT14 7LF
Tel: +44 (0)1784 440088
Fax:+44 (0)870 7053252
Email:forall@sesameaccess.com
Web:www.sesameaccess.com


Project name: 1588.America Street, No.1
Drawing pack: 1588.America Street, No.1_EngineeringDrawing.dwg
Process type: C - cutting W - Welding A - Assembly

Revision 0


Sheet 3 / 12

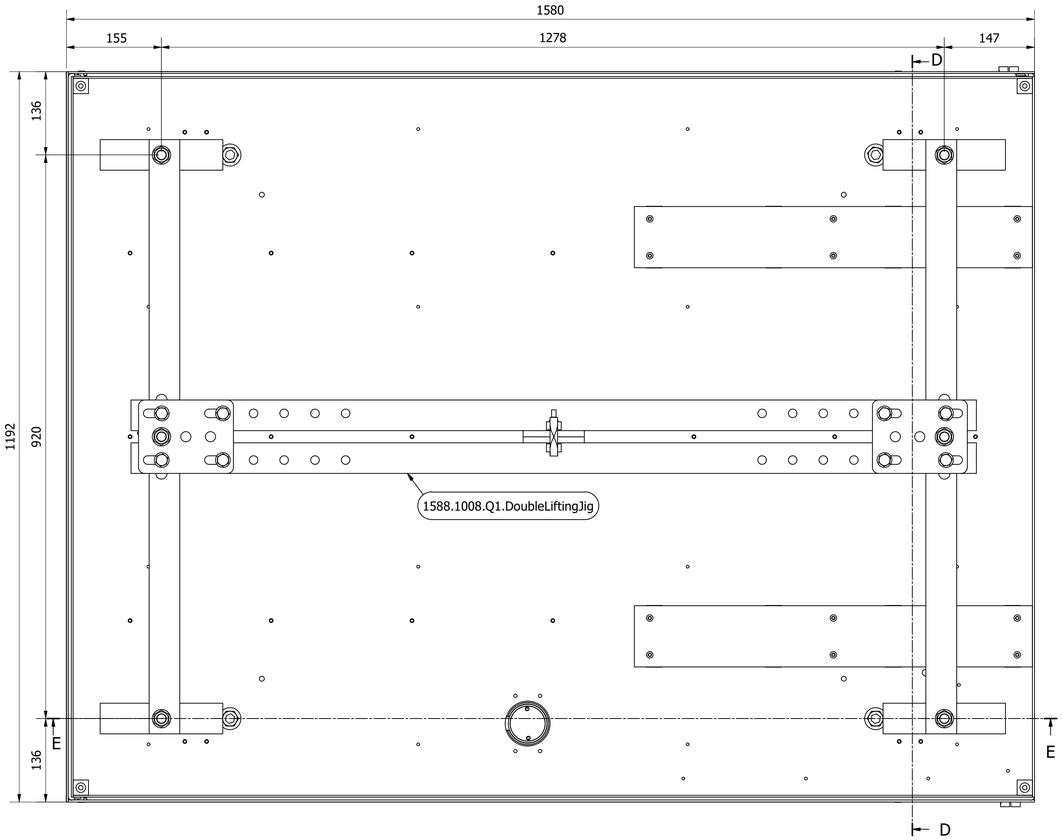


D-D (1 : 5)

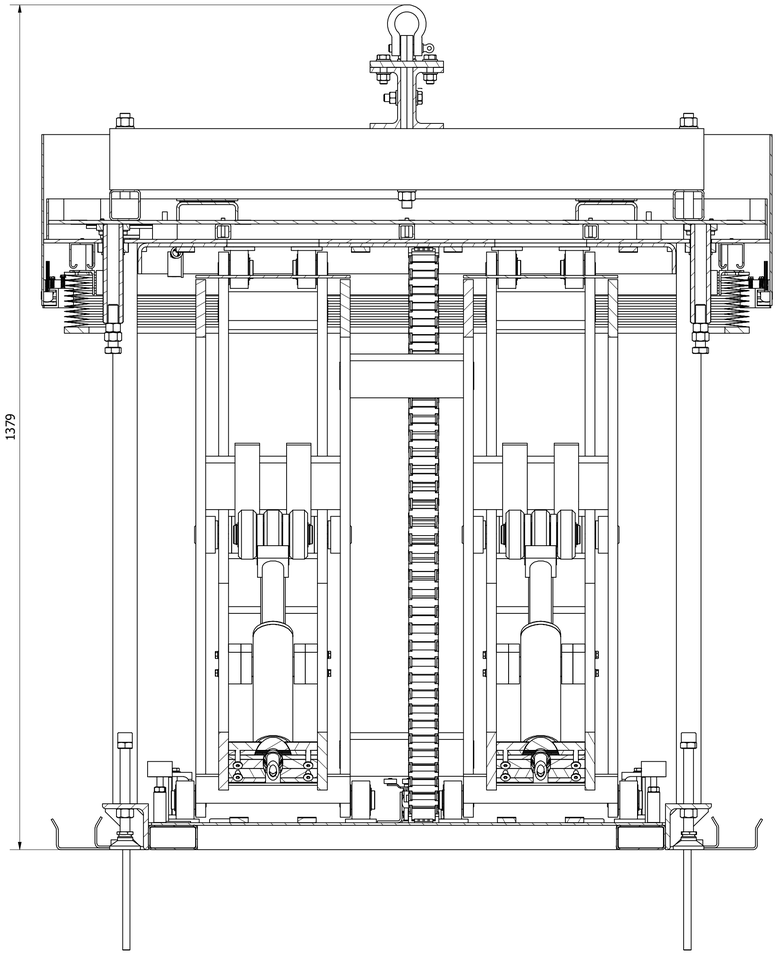


1588.1008.Q1.DoubleLiftingJig (1 : 10)

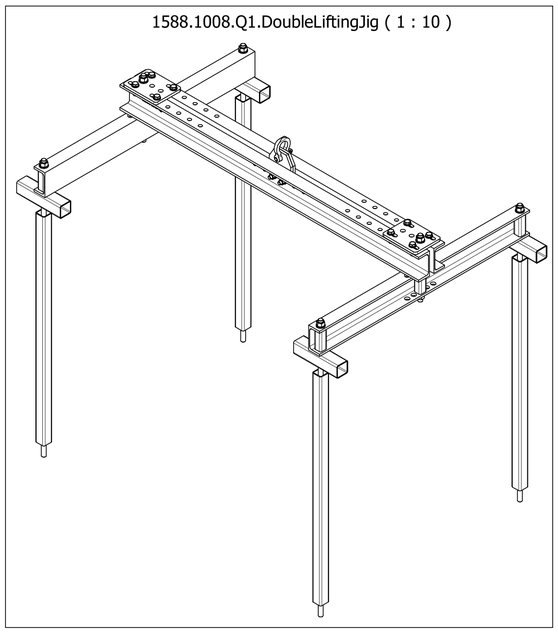

E-E (1 : 5)

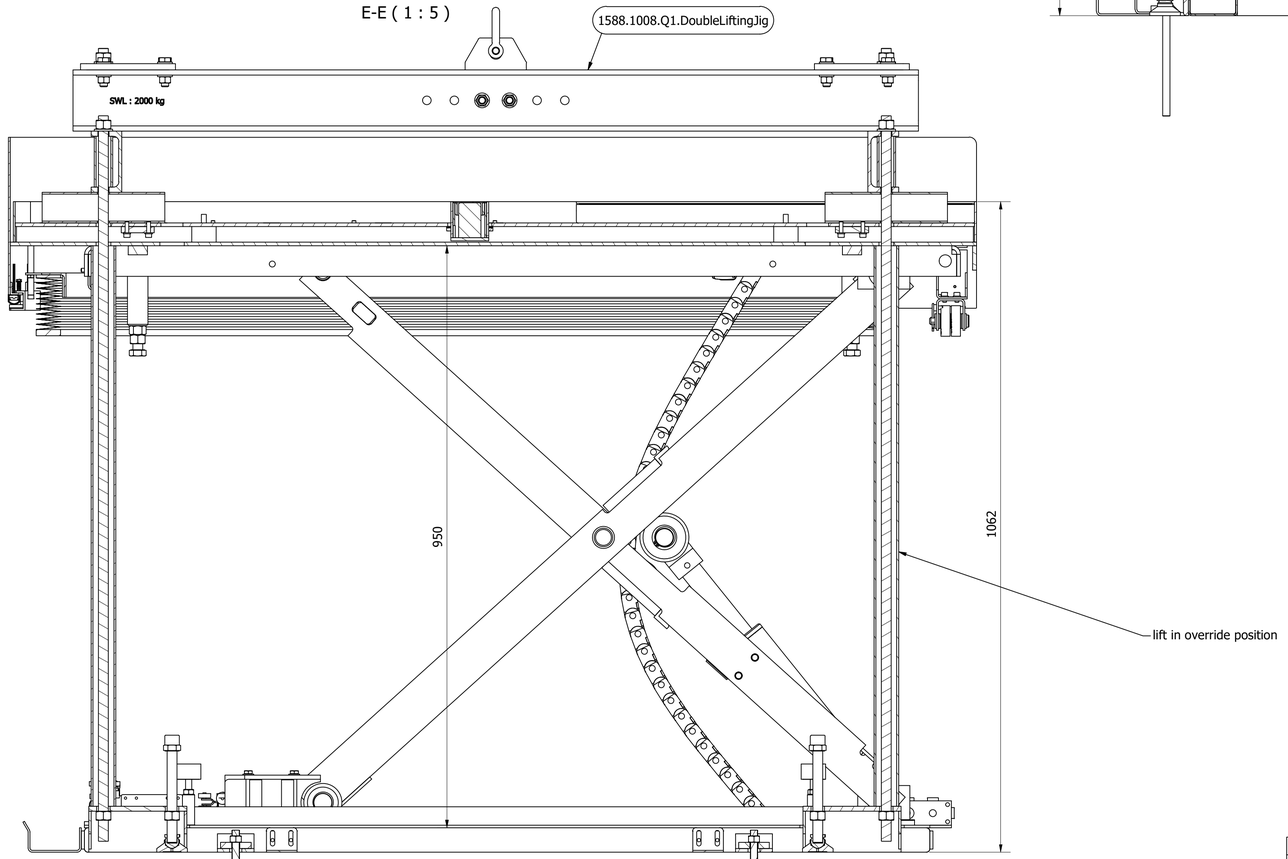

1588.America Street, No.1 (1 : 11)
Stage 2

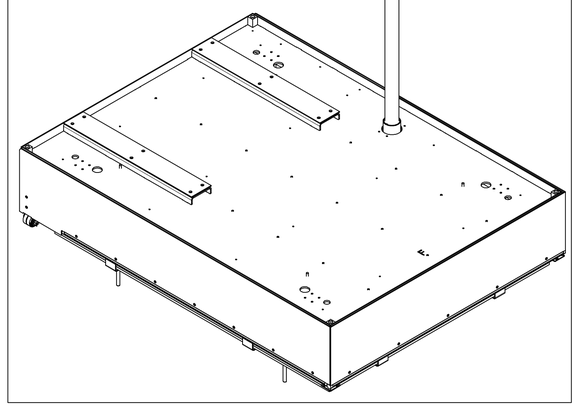

1588.America Street, No.1
Stage 3 Platform Assembly
Required parts on the right side

PARTS LIST					
ITEM	QTY	PART NUMBER	DESCRIPTION	MATERIAL	VENDOR
1	1	1588.1008.Q1.DoubleLiftingJig	Four points lifting jig		Sesame
2	1	1588.America Street, No. 1	Stage 2		Sesame

Parts for:
1588.America Street, No.1
Stage 3 Platform Assembly

PARTS LIST					
ITEM	QTY	PART NUMBER	DESCRIPTION	MATERIAL	VENDOR
1	1	1588.1008.Q1.DoubleLiftingJig	Four points lifting jig		Sesame
2	1	1588.America Street, No. 1	Stage 2		Sesame


This drawing and the information it contains is the property of Sesame Access Systems LTD. and must not be copied or issued to any third party


Drawn by: IDSPC7
Checked by: S.J.Lyons
Date: 14/07/2026

Sesame ACCESS FOR ALL
Unit 1, Cumberland Works
Wintersell Business Park
Surrey, KT14 7LF
Tel: +44 (0)1784 440088
Fax:+44 (0)870 7053252
Email:forall@sesameaccess.com
Web:www.sesameaccess.com


Project name: 1588.America Street, No.1
Drawing pack: 1588.America Street, No.1_EngineeringDrawing.dwg
Process type: C - cutting W - Welding A - Assembly

Revision 0

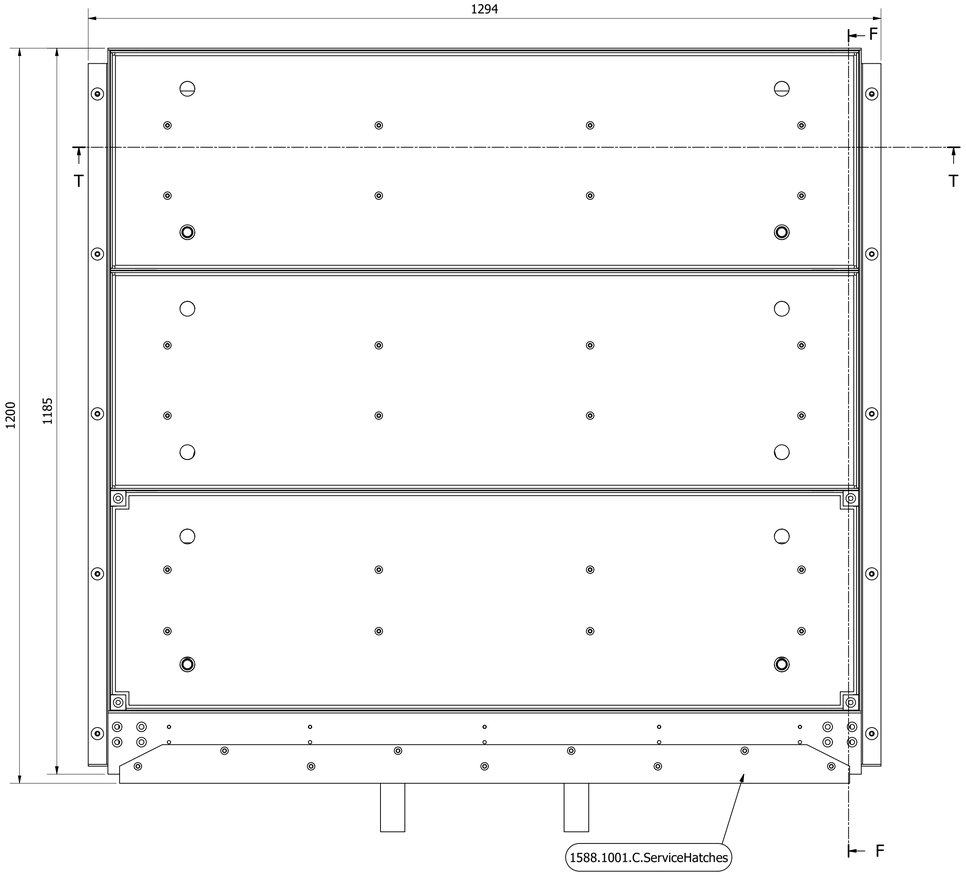


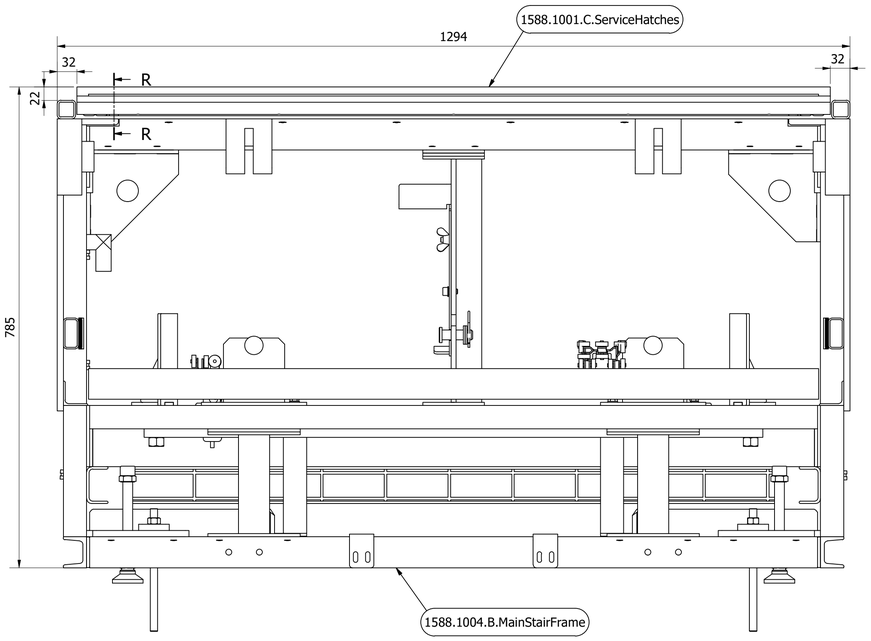


F-F (1 : 5)

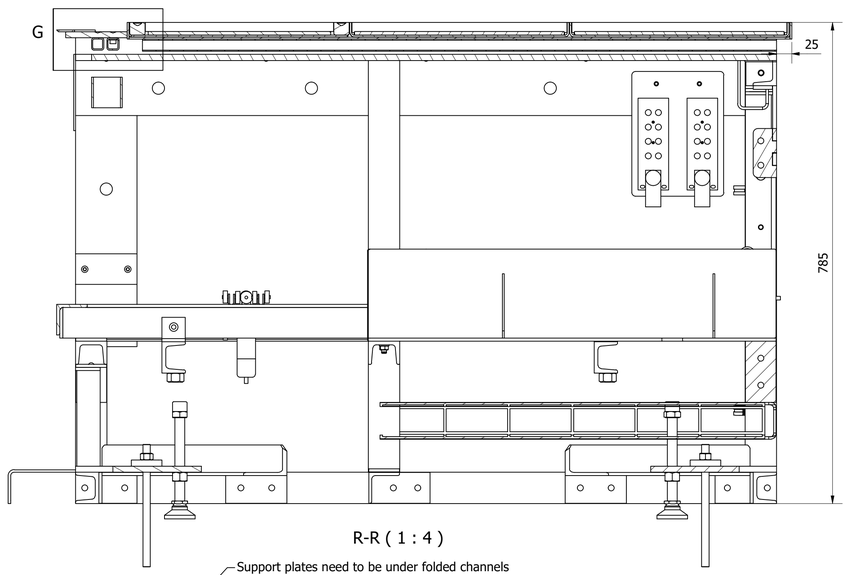


R-R (1 : 4)

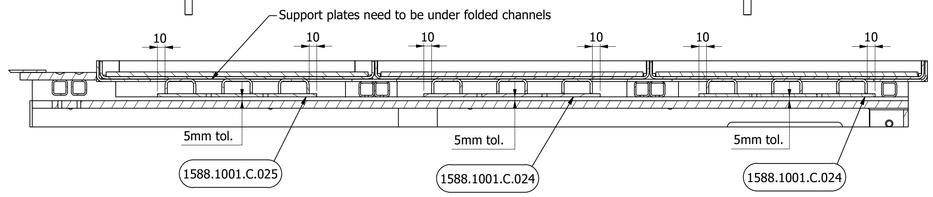


T-T (1 : 4)

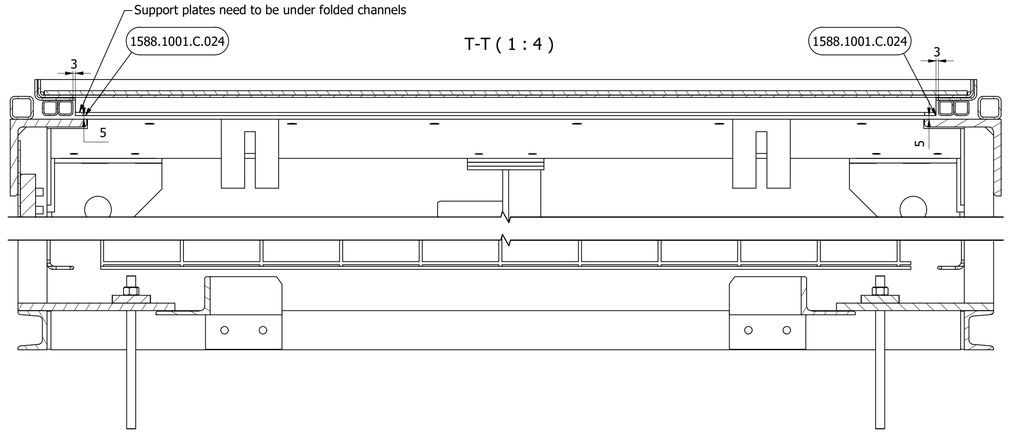


G (1 : 1)

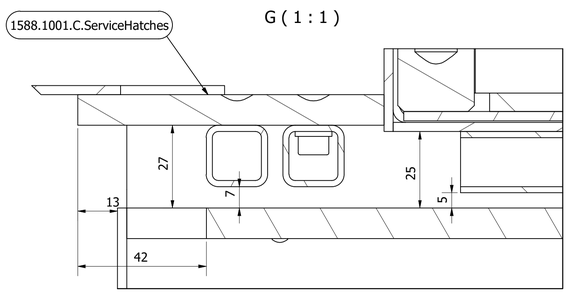



1588.1001.C.ServiceHatches (1 : 10)

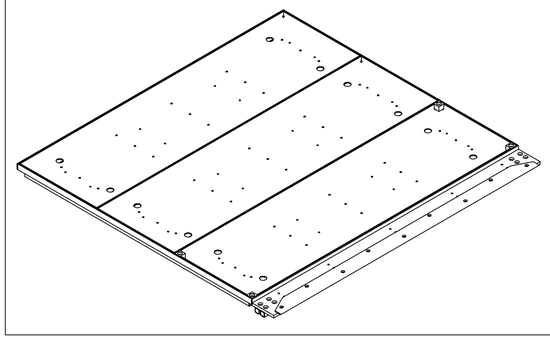

1588.1004.B.MainStairFrame (1 : 10)

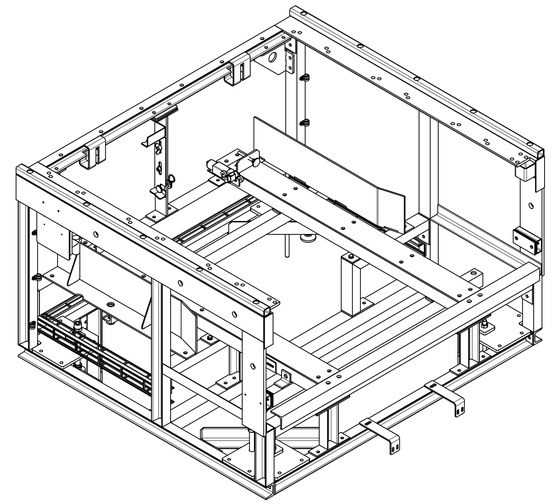

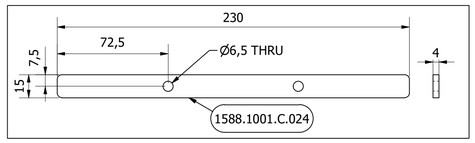

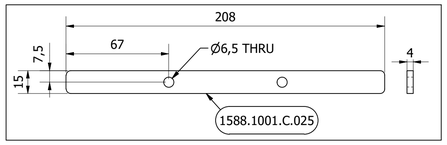

1588.America Street, No.1
Stage 4 Stairs Assembly
Required parts on the right side

PARTS LIST					
ITEM	QTY	PART NUMBER	DESCRIPTION	MATERIAL	VENDOR
1	4	1588.1001.C.024	Support	Stainless Steel	Laser Cut
2	2	1588.1001.C.025	Support	Stainless Steel	Laser Cut
3	1	1588.1001.C.ServiceHatches	Service hatch		Sesame
4	1	1588.1004.B.MainStairFrame	Stair frame		Sesame

Parts for:
1588.America Street, No.1
Stage 4 Stairs Assembly

PARTS LIST					
ITEM	QTY	PART NUMBER	DESCRIPTION	MATERIAL	VENDOR
1	4	1588.1001.C.024	Support	Stainless Steel	Laser Cut
2	2	1588.1001.C.025	Support	Stainless Steel	Laser Cut
3	1	1588.1001.C.ServiceHatches	Service hatch		Sesame
4	1	1588.1004.B.MainStairFrame	Stair frame		Sesame

This drawing and the information it contains is the property of Sesame Access Systems LTD. and must not be copied or issued to any third party


Drawn by: IDSPC7
Checked by: S.J.Lyons
Date: 14/07/2026

Sesame ACCESS FOR ALL
Unit 1, Cumberland Works
Wintersell Business Park
Surrey, KT14 7LF
Tel: +44 (0)1784 440088
Fax:+44 (0)870 7053252
Email:forall@sesameaccess.com
Web:www.sesameaccess.com


Project name: 1588.America Street, No.1
Drawing pack: 1588.America Street, No.1_EngineeringDrawing.dwg
Process type: C - cutting W - Welding A - Assembly


Revision: 0

Sheet: 5 / 12

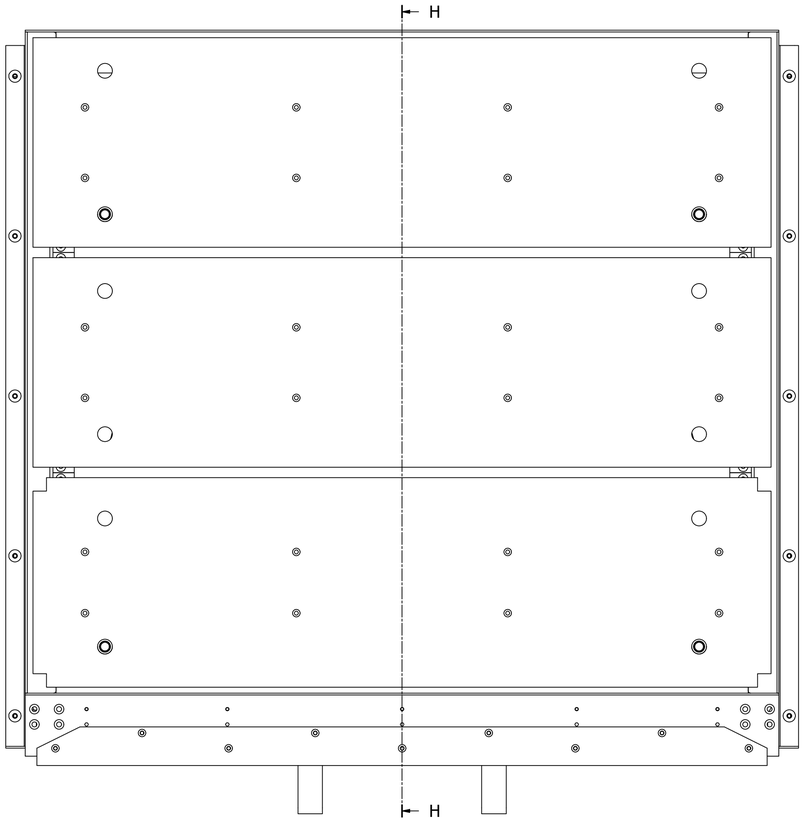


H-H (1 : 5)

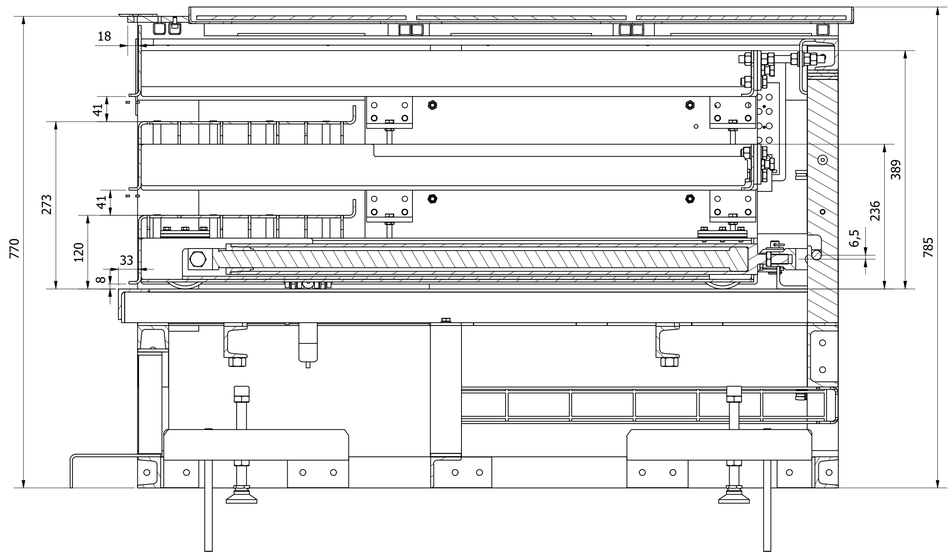


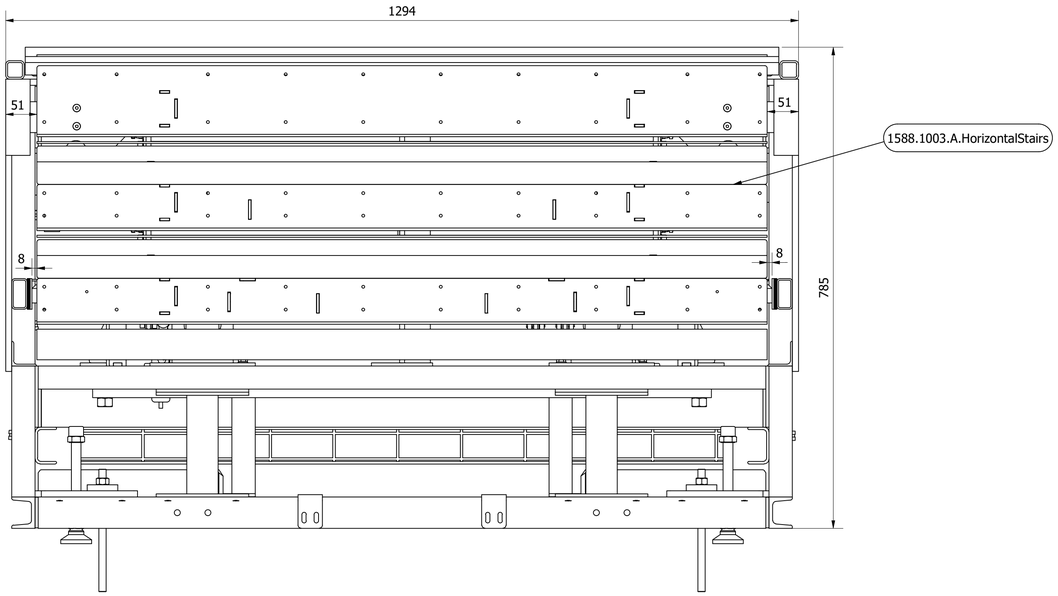

1588.America Street, No.1 (1 : 10)
Stage 4

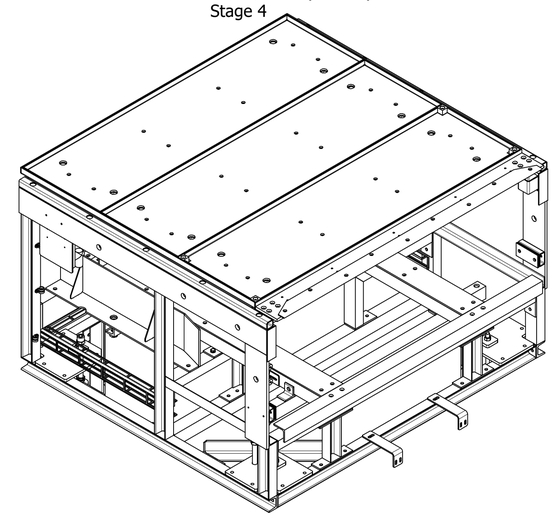

1588.1003.A.HorizontalStairs (1 : 10)

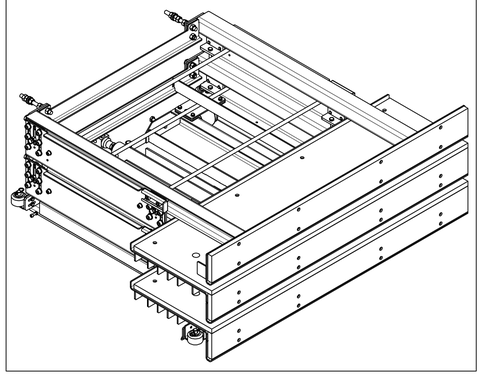

1588.America Street, No.1
Stage 5 Stairs Assembly
Required parts on the right side

PARTS LIST					
ITEM	QTY	PART NUMBER	DESCRIPTION	MATERIAL	VENDOR
1	1	1588.1003.A.HorizontalStairs	Main Assembly		Sesame
2	1	1588.America Street, No. 1	Stage 4		Sesame

Parts for:
1588.America Street, No.1
Stage 5 Stairs Assembly

PARTS LIST					
ITEM	QTY	PART NUMBER	DESCRIPTION	MATERIAL	VENDOR
1	1	1588.1003.A.HorizontalStairs	Main Assembly		Sesame
2	1	1588.America Street, No. 1	Stage 4		Sesame

This drawing and the information it contains is the property of Sesame Access Systems LTD. and must not be copied or issued to any third party


Drawn by: IDSPC7
Checked by: S.J.Lyons
Date: 14/07/2026

Sesame ACCESS FOR ALL
Unit 1, Cumberland Works
Wintersell Business Park
Surrey, KT14 7LF
Tel: +44 (0)1784 440088
Fax:+44 (0)870 7053252
Email:forall@sesameaccess.com
Web:www.sesameaccess.com


Project name: 1588.America Street, No.1
Drawing pack: 1588.America Street, No.1_EngineeringDrawing.dwg
Process type: C - cutting W - Welding A - Assembly

Revision: 0


Sheet: 6 / 12

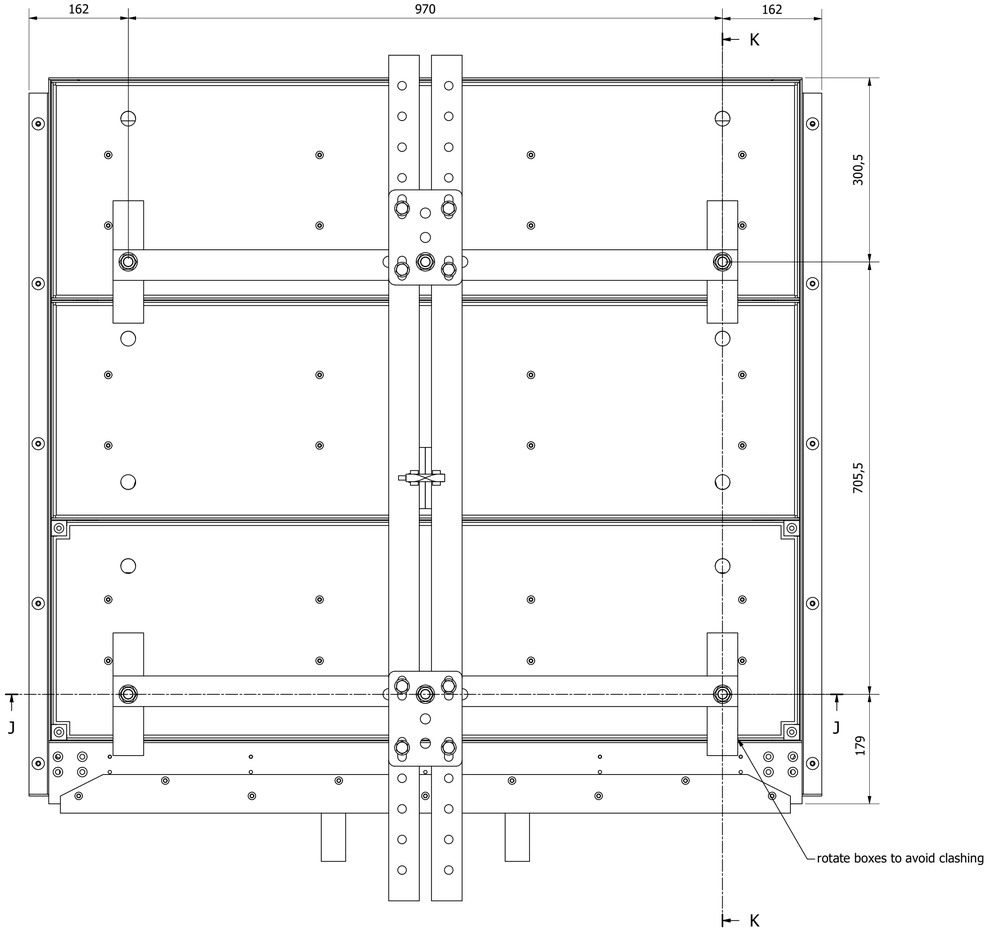


J-J (1 : 5)

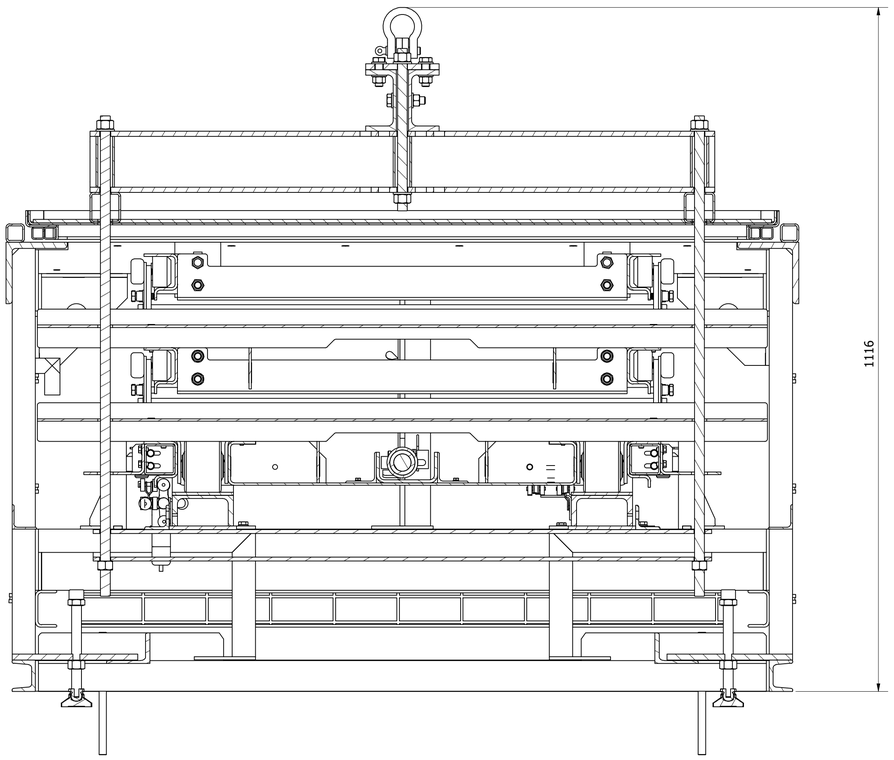


K-K (1 : 5)

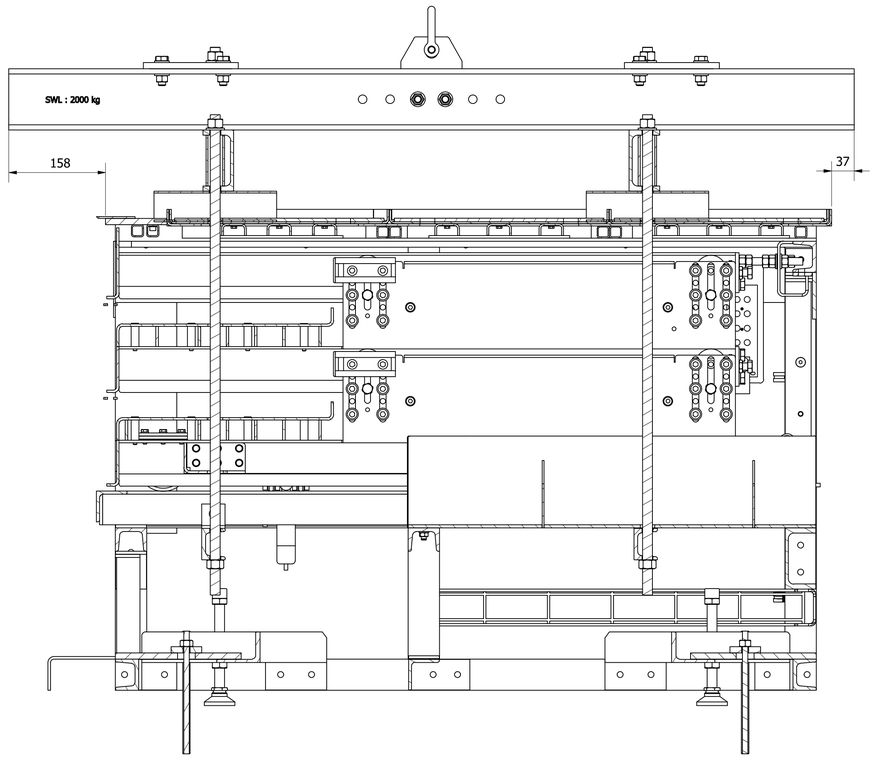

1588.America Street, No.1 (1 : 10)
Stage 5

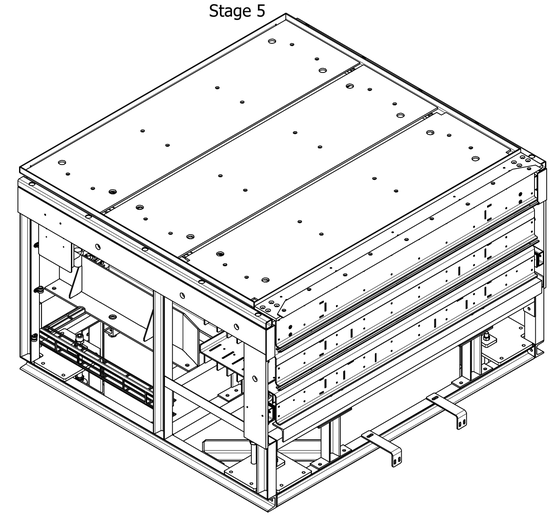

1588.1008.Q1.DoubleLiftingJig_2 (1 : 10)

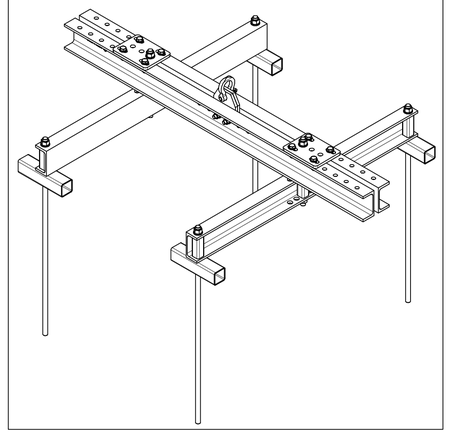

1588.America Street, No.1
Stage 6 Stairs Assembly
Required parts on the right side

PARTS LIST					
ITEM	QTY	PART NUMBER	DESCRIPTION	MATERIAL	VENDOR
1	1	1588.1008.Q1.DoubleLiftingJig_2	Four points lifting jig		Sesame
2	1	1588.America Street, No. 1	Stage 5		Sesame

Parts for:
1588.America Street, No.1
Stage 6 Stairs Assembly

PARTS LIST					
ITEM	QTY	PART NUMBER	DESCRIPTION	MATERIAL	VENDOR
1	1	1588.1008.Q1.DoubleLiftingJig_2	Four points lifting jig		Sesame
2	1	1588.America Street, No. 1	Stage 5		Sesame


This drawing and the information it contains is the property of Sesame Access Systems LTD. and must not be copied or issued to any third party


Drawn by: IDSPC7
Checked by: S.J.Lyons
Date: 14/07/2026


Sesame ACCESS FOR ALL
Unit 1, Cumberland Works
Wintersett Business Park
Surrey, KT14 7LF
Tel: +44 (0)1784 440088
Fax:+44 (0)870 7053252
Email:forall@sesameaccess.com
Web:www.sesameaccess.com

Project name: 1588.America Street, No.1
Drawing pack: 1588.America Street, No.1_EngineeringDrawing.dwg
Process type: C - cutting W - Welding A - Assembly


Revision: 0

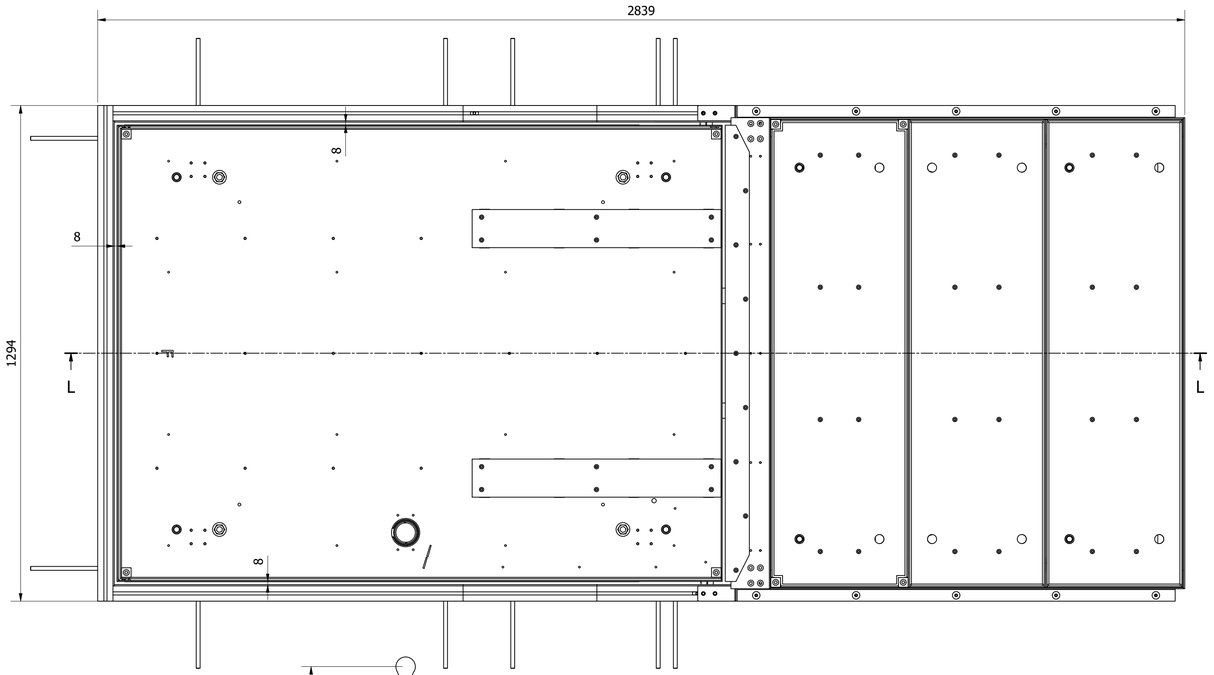

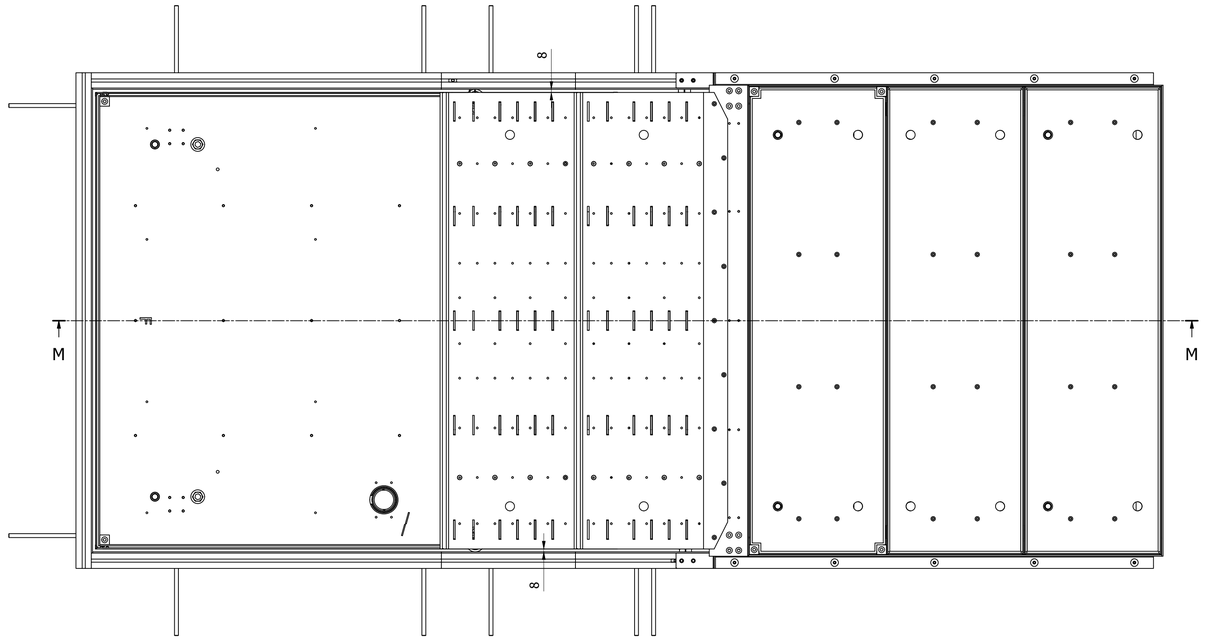


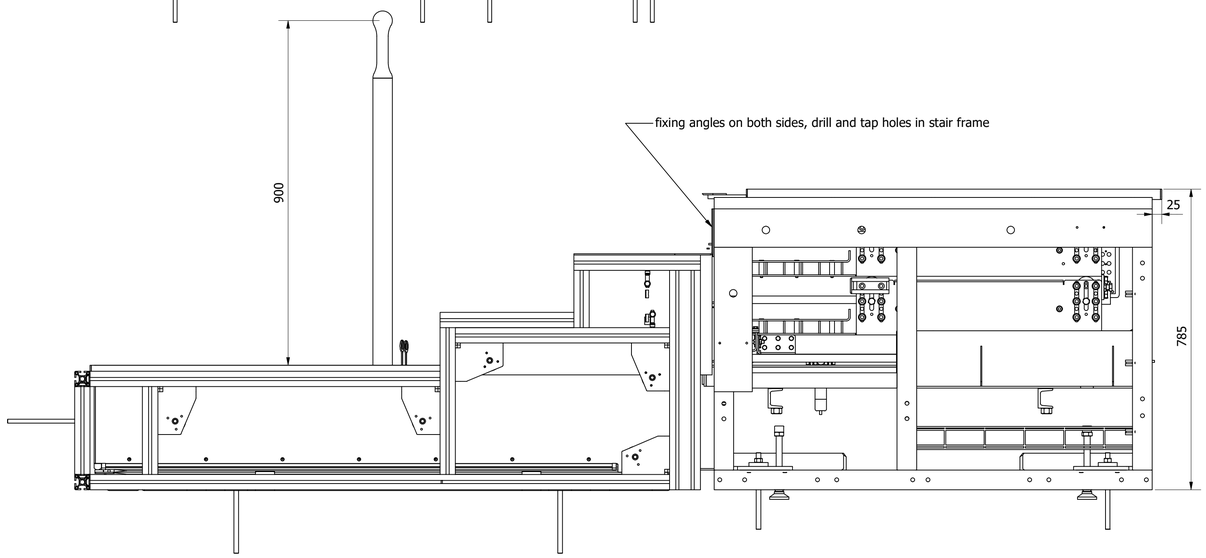

M-M (1 : 8)

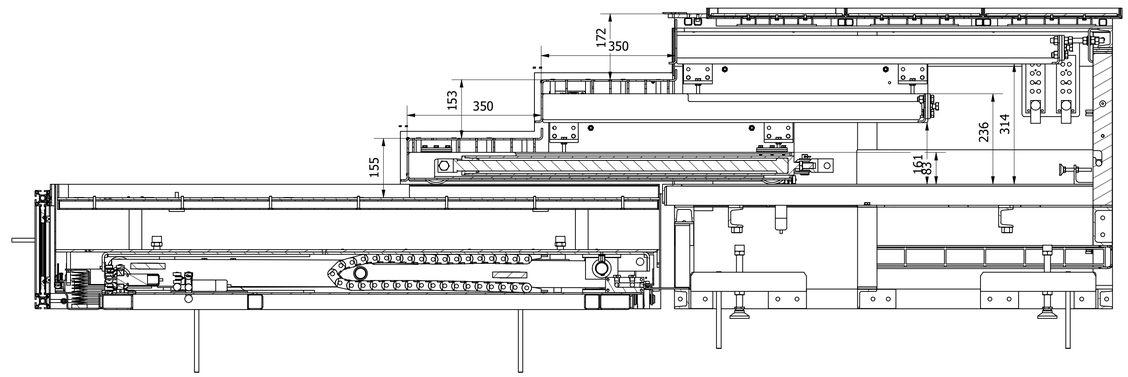

L-L (1 : 8)

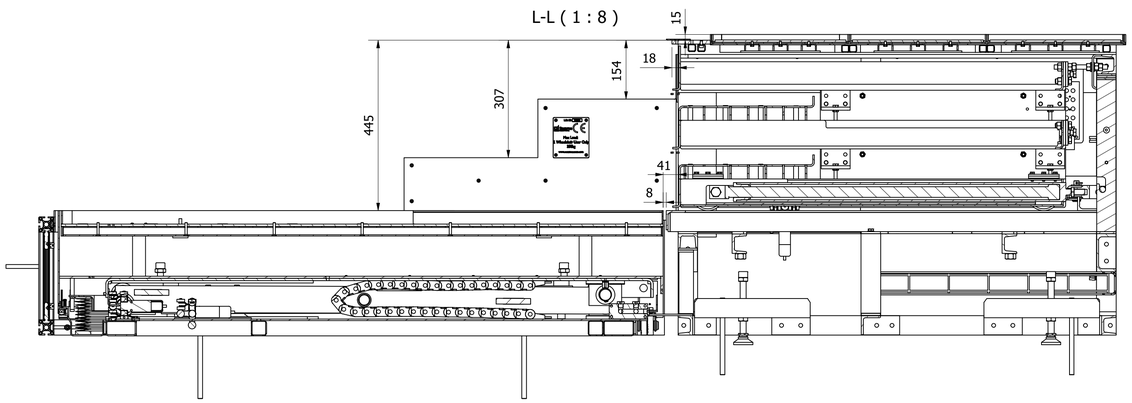

QC Page 1/2

1588.America Street, No.1
Total Rise: 460mm
Total Mass: 1450kg (According to 3D model)
Platform Mass: 750kg (According to 3D model)
Stairs Mass: 650kg (According to 3D model)
Pit Trim: 50kg (According to 3D model)


This drawing and the information it contains is the property of Sesame Access Systems LTD. and must not be copied or issued to any third party

Drawn by	Checked by	Date:	Project name:	Revision
IDSPC7	S.J.Lyons	14/07/2026	1588.America Street, No.1	0


Sesame ACCESS FOR ALL
Unit 1, Cumberland Works
Wintersell Business Park
Surrey, KT14 7LF
Tel: +44 (0)1784 440088
Fax:+44 (0)870 7053252
Email:forall@sesameaccess.com
Web:www.sesameaccess.com

Drawing pack: 1588.America Street, No.1_EngineeringDrawing.dwg

Process type: C - cutting W - Welding A - Assembly

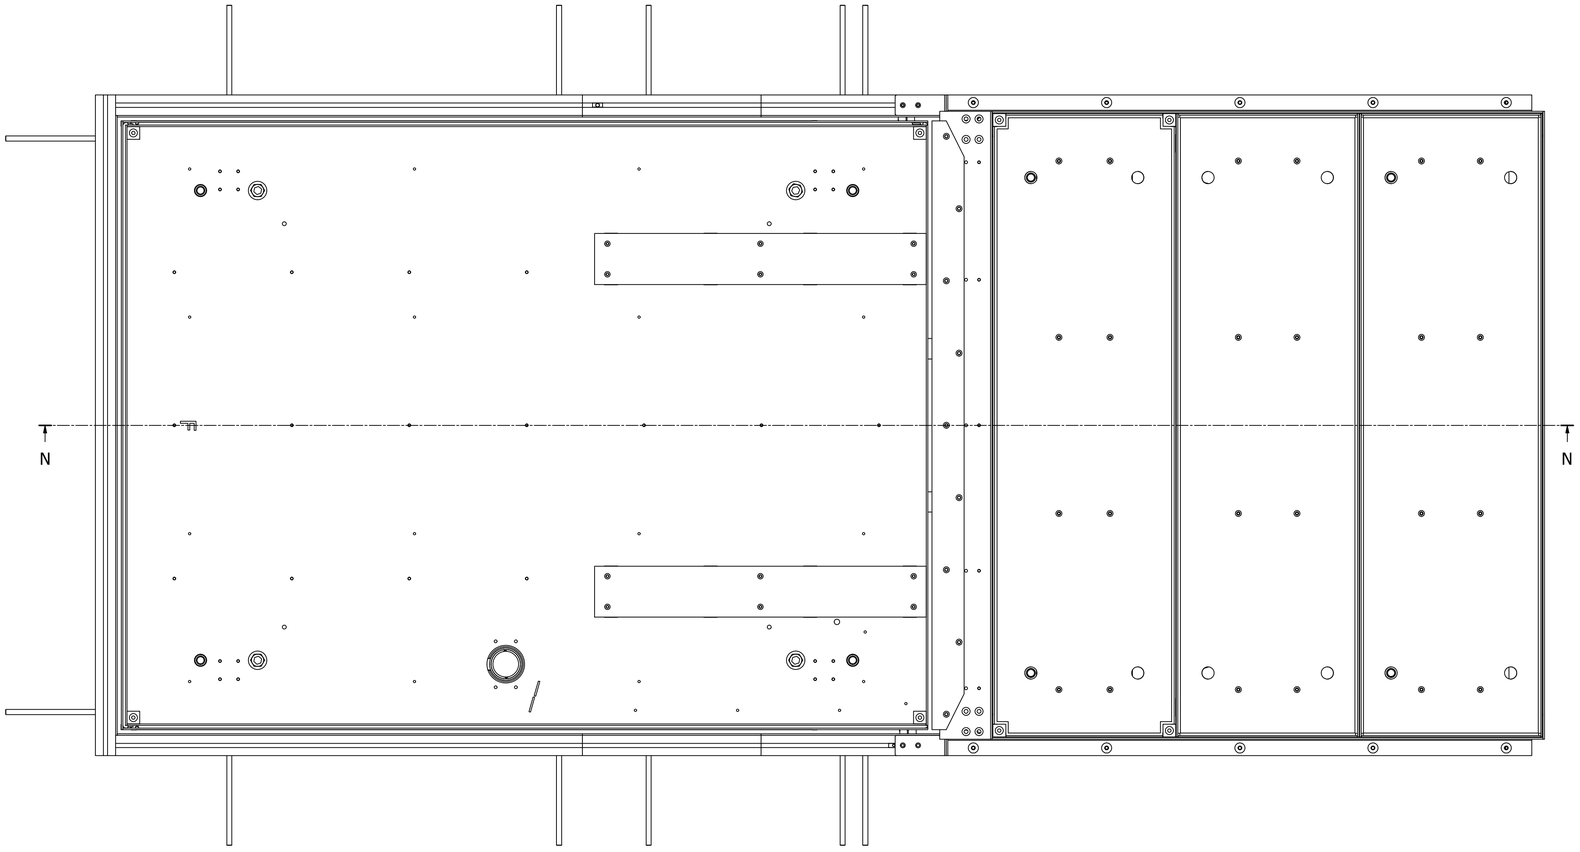

N-N (1 : 6)

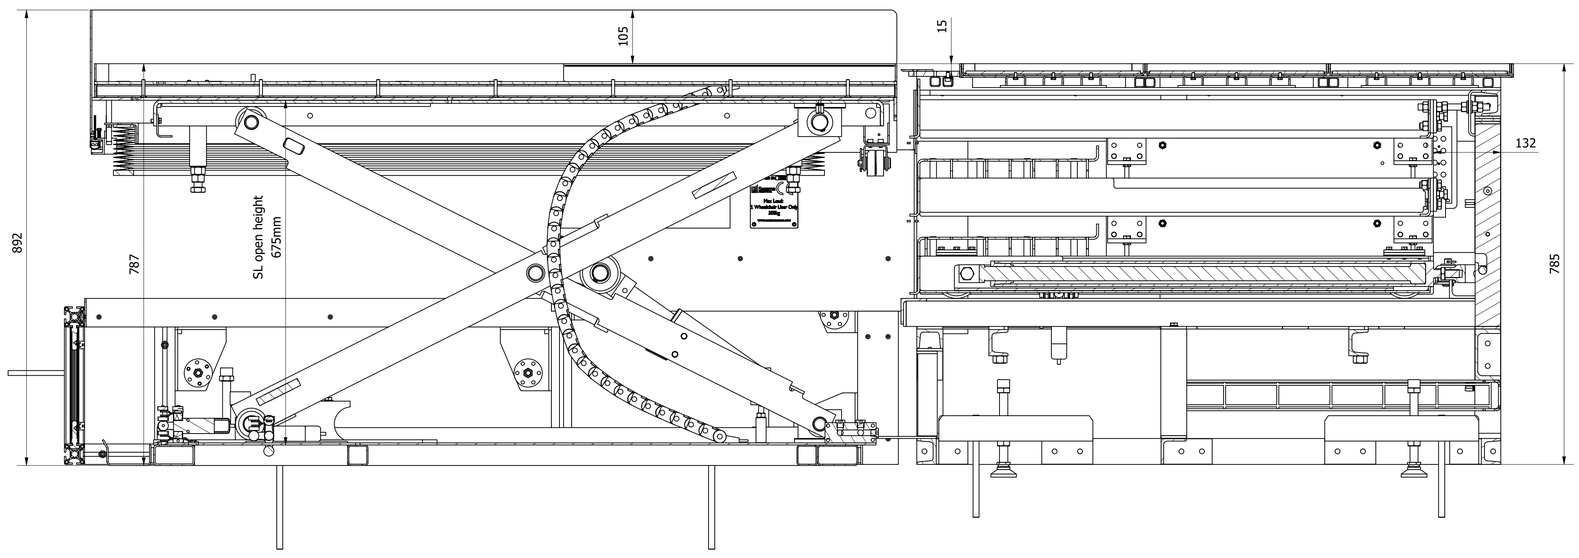

QC Page 2/2

1588.America Street, No.1
Total Rise: 460mm
Total Mass: 1450kg (According to 3D model)
Platform Mass: 750kg (According to 3D model)
Stairs Mass: 650kg (According to 3D model)
Pit Trim: 50kg (According to 3D model)

Cladding used in project:
Surrounding Sesame System:
*Upper Landing: 3 mm cladding + 12 mm bedding
*Step Risers: 20 mm cladding + 15 mm bedding
*Step Treads: 20 mm cladding + 15 mm bedding
*Lower Landing: 20 mm cladding + 15 mm bedding

Cladding used in project:
On Sesame System:
Service Hatches: 3 mm cladding +2mm tol. + 12 mm Cement Board
Step Risers: 20 mm cladding + 5 mm flexible adhesive + 18 mm Cement Board
Step Treads: 20 mm cladding + 5 mm flexible adhesive + 10 mm Cement Board
Platform: 20 mm cladding + 5 mm flexible adhesive + 10mm Cement Board

This drawing and the information it contains is the property of Sesame Access Systems LTD. and must not be copied or issued to any third party

Drawn by	Checked by	Date:	Project name:	Revision
IDSPC7	S.J.Lyons	14/07/2026	1588.America Street, No.1	0

Sesame ACCESS FOR ALL
Unit 1, Cumberland Works
Wintersell Business Park
Surrey, KT14 7LF
Tel: +44 (0)1784 440088
Fax:+44 (0)870 7053252
Email:forall@sesameaccess.com
Web:www.sesameaccess.com

Drawing pack: 1588.America Street, No.1_EngineeringDrawing.dwg


Process type: C - cutting W - Welding A - Assembly

Sheet 9 / 12


To be taken on Site 1/3

- Button Stations
- Safety Working Load Plate
- PLC
- Sesame Keys
- CAT 5 cable length TBC by Steven
- Button Station Cable TBC by Steven
- Lifting Jigs
- Studding M10x200 (36off) + washers and nuts
- Job Specific Packers Stainless Steel(double check with Steven) 200x100x10,5,3,2,1,
- Tool for Lift Frame Leveling
- Cement boards (on the next pages)
- KeyFob


1588.1008.D1.MachineRoomCabinet (1 : 10)

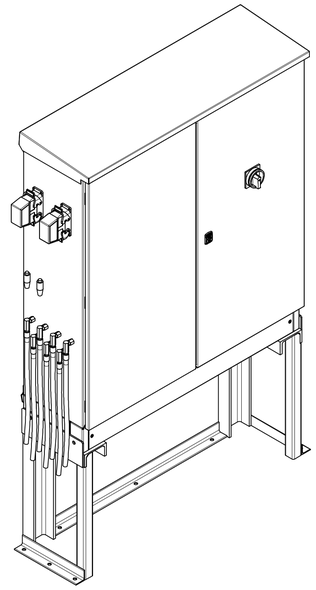


Button Station Cable (1 : 2)

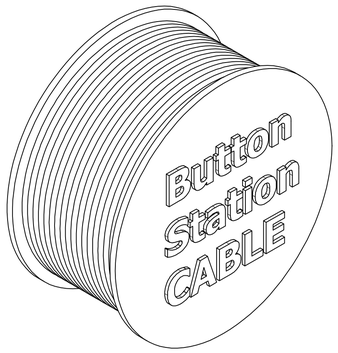


CAT 5 Cable (1 : 2)

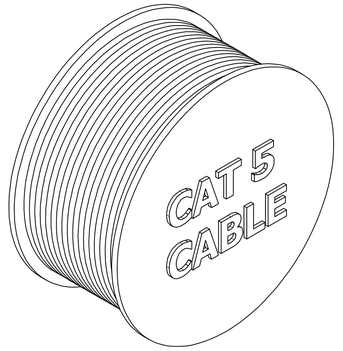


Sesame Keys (1 : 1)

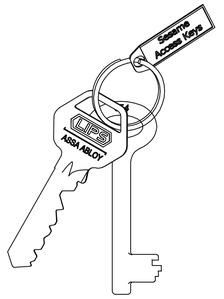


1588.1008.Q1.DoubleLiftingJig_2 (1 : 10)

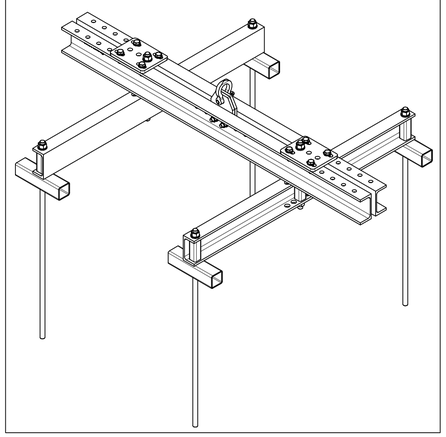


1588.1002.G.MT.PitTrimSmall (1 : 10)

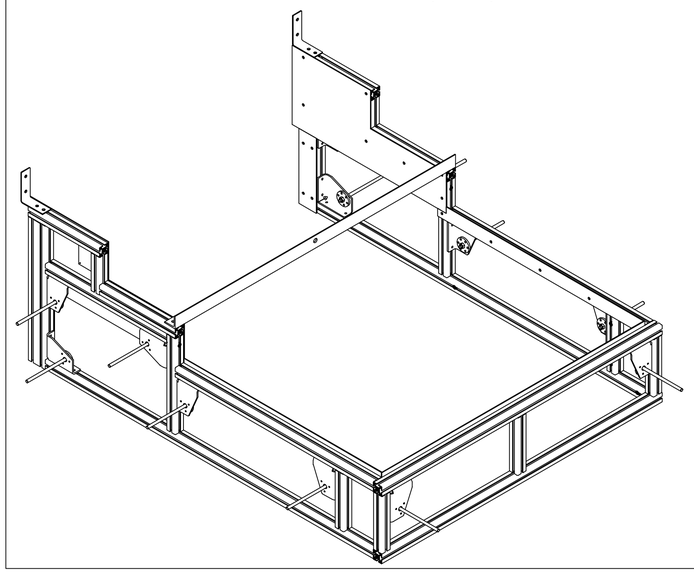

1588.1016.BS.1 (1 : 1,5)

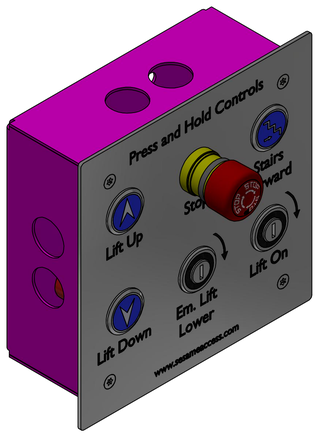

1588.1008.Q1.DoubleLiftingJig (1 : 10)

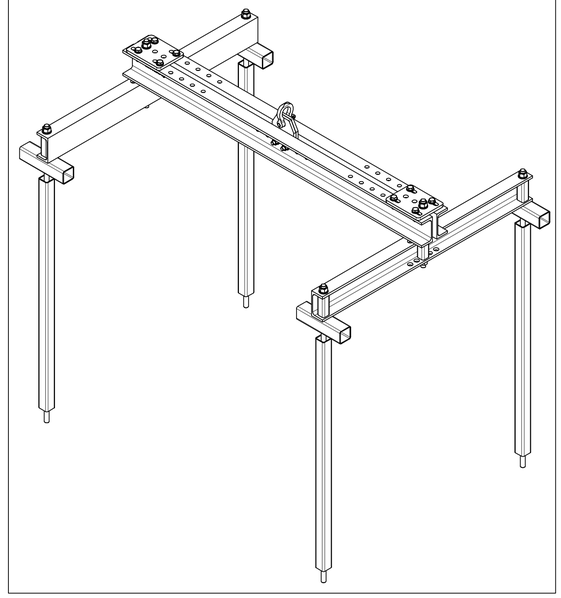


This drawing and the information it contains is the property of Sesame Access Systems LTD. and must not be copied or issued to any third party


Drawn by	Checked by	Date:	Project name:	Revision
IDSPC7	S.J.Lyons	14/07/2026	1588.America Street, No.1	0


Sesame ACCESS FOR ALL
Unit 1, Cumberland Works
Wintersell Business Park
Surrey, KT14 7LF
Tel: +44 (0)1784 440088
Fax:+44 (0)870 7053252
Email:forall@sesameaccess.com
Web:www.sesameaccess.com

Drawing pack: 1588.America Street, No.1_EngineeringDrawing.dwg

Process type: C - cutting, W - Welding, A - Assembly

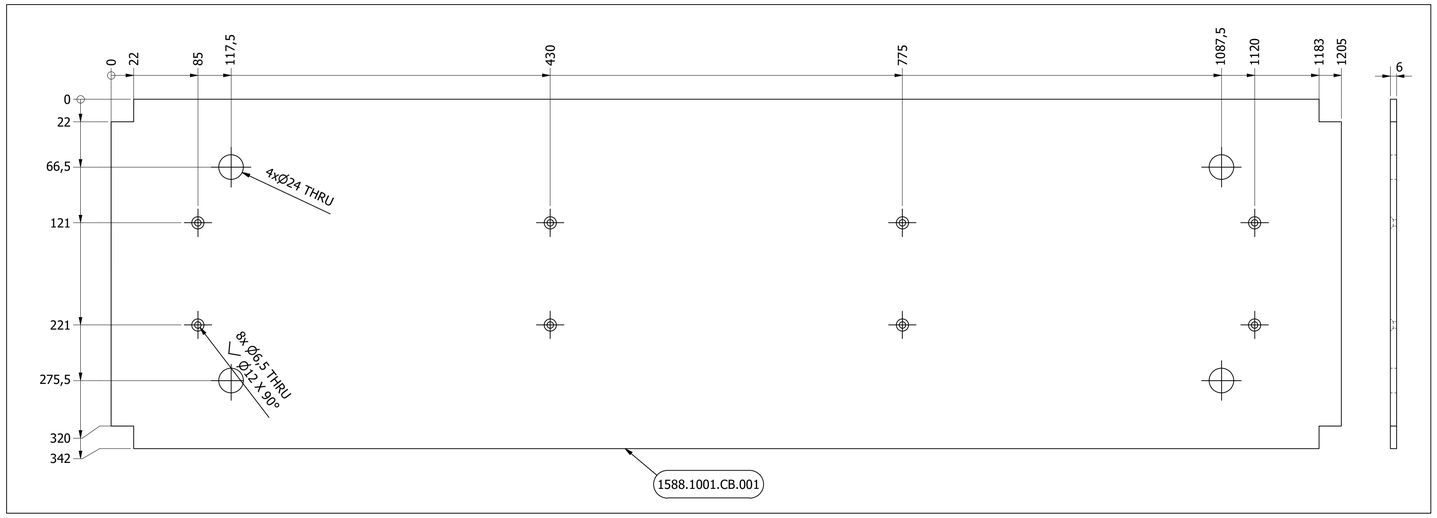

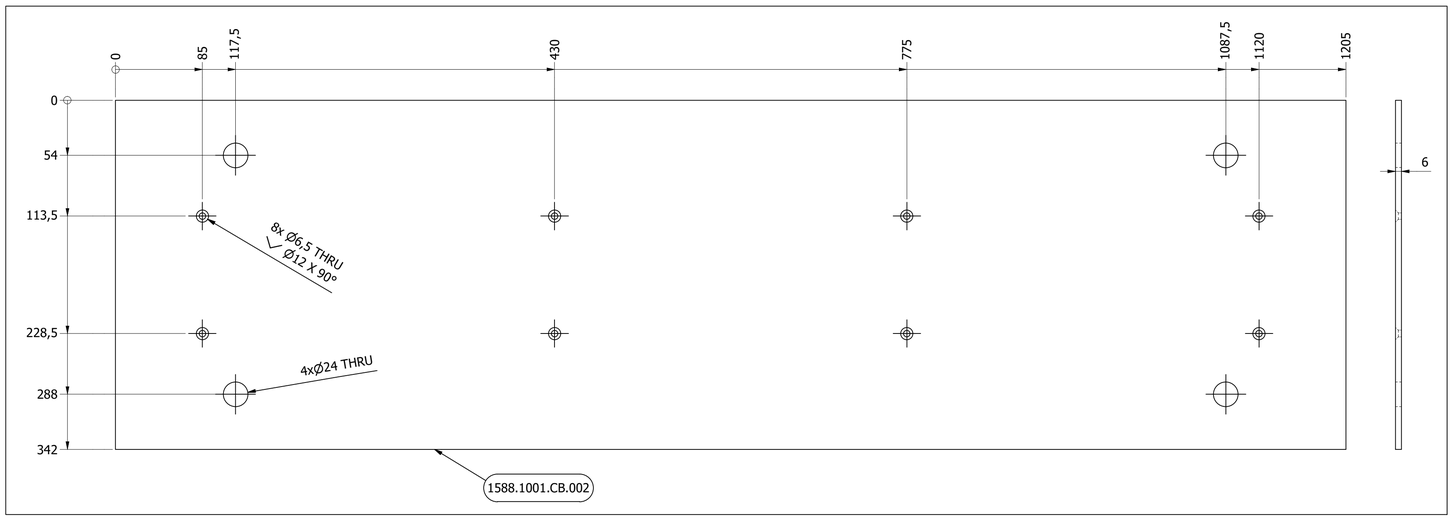

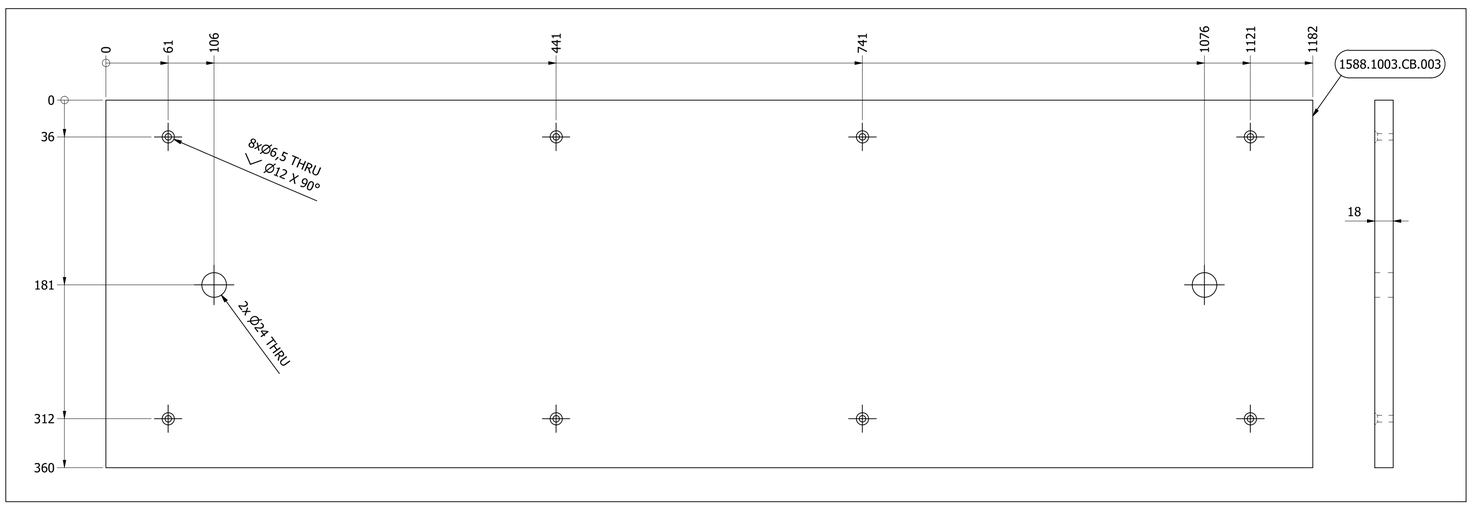

To be taken on Site 2/3

- Cement boards

This drawing and the information it contains is the property of Sesame Access Systems LTD. and must not be copied or issued to any third party


Drawn by	Checked by	Date:	Project name:	Revision
IDSPC7	S.J.Lyons	14/07/2026	1588.America Street, No.1	0


Sesame ACCESS FOR ALL
Unit 1, Cumberland Works
Wintersell Business Park
Surrey, KT14 7LF
Tel: +44 (0)1784 440088
Fax:+44 (0)870 7053252
Email:forall@sesameaccess.com
Web:www.sesameaccess.com


Drawing pack: 1588.America Street, No.1_EngineeringDrawing.dwg

Process type: C - cutting W - Welding A - Assembly

Sheet 11 / 12

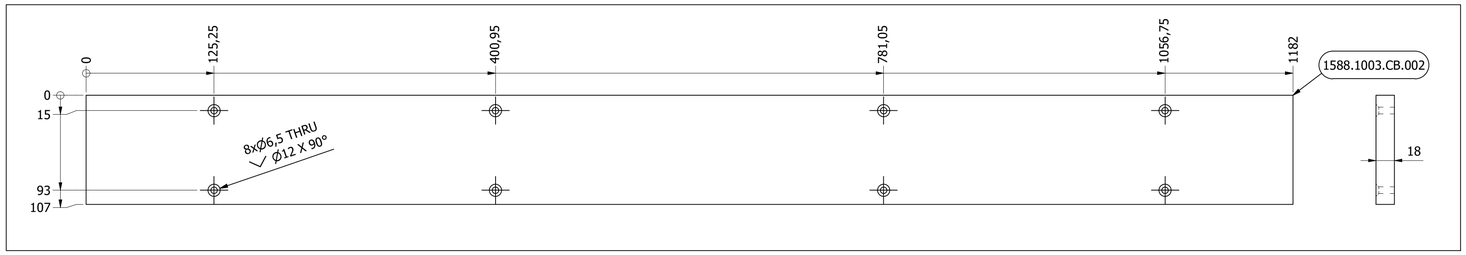

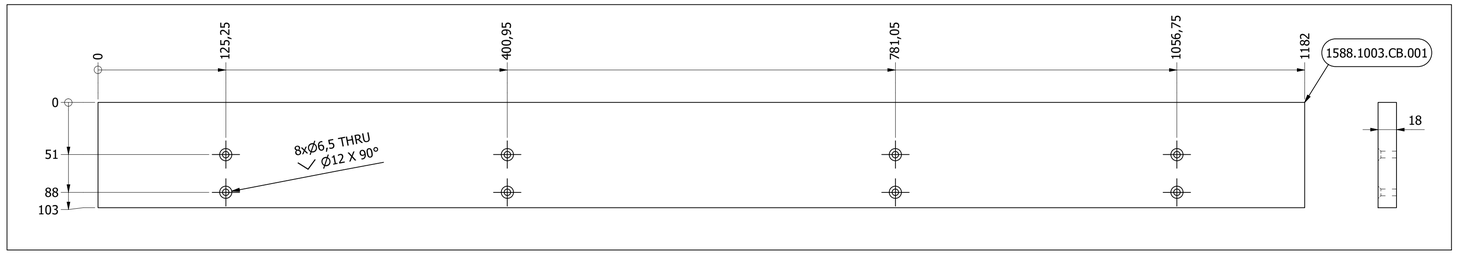

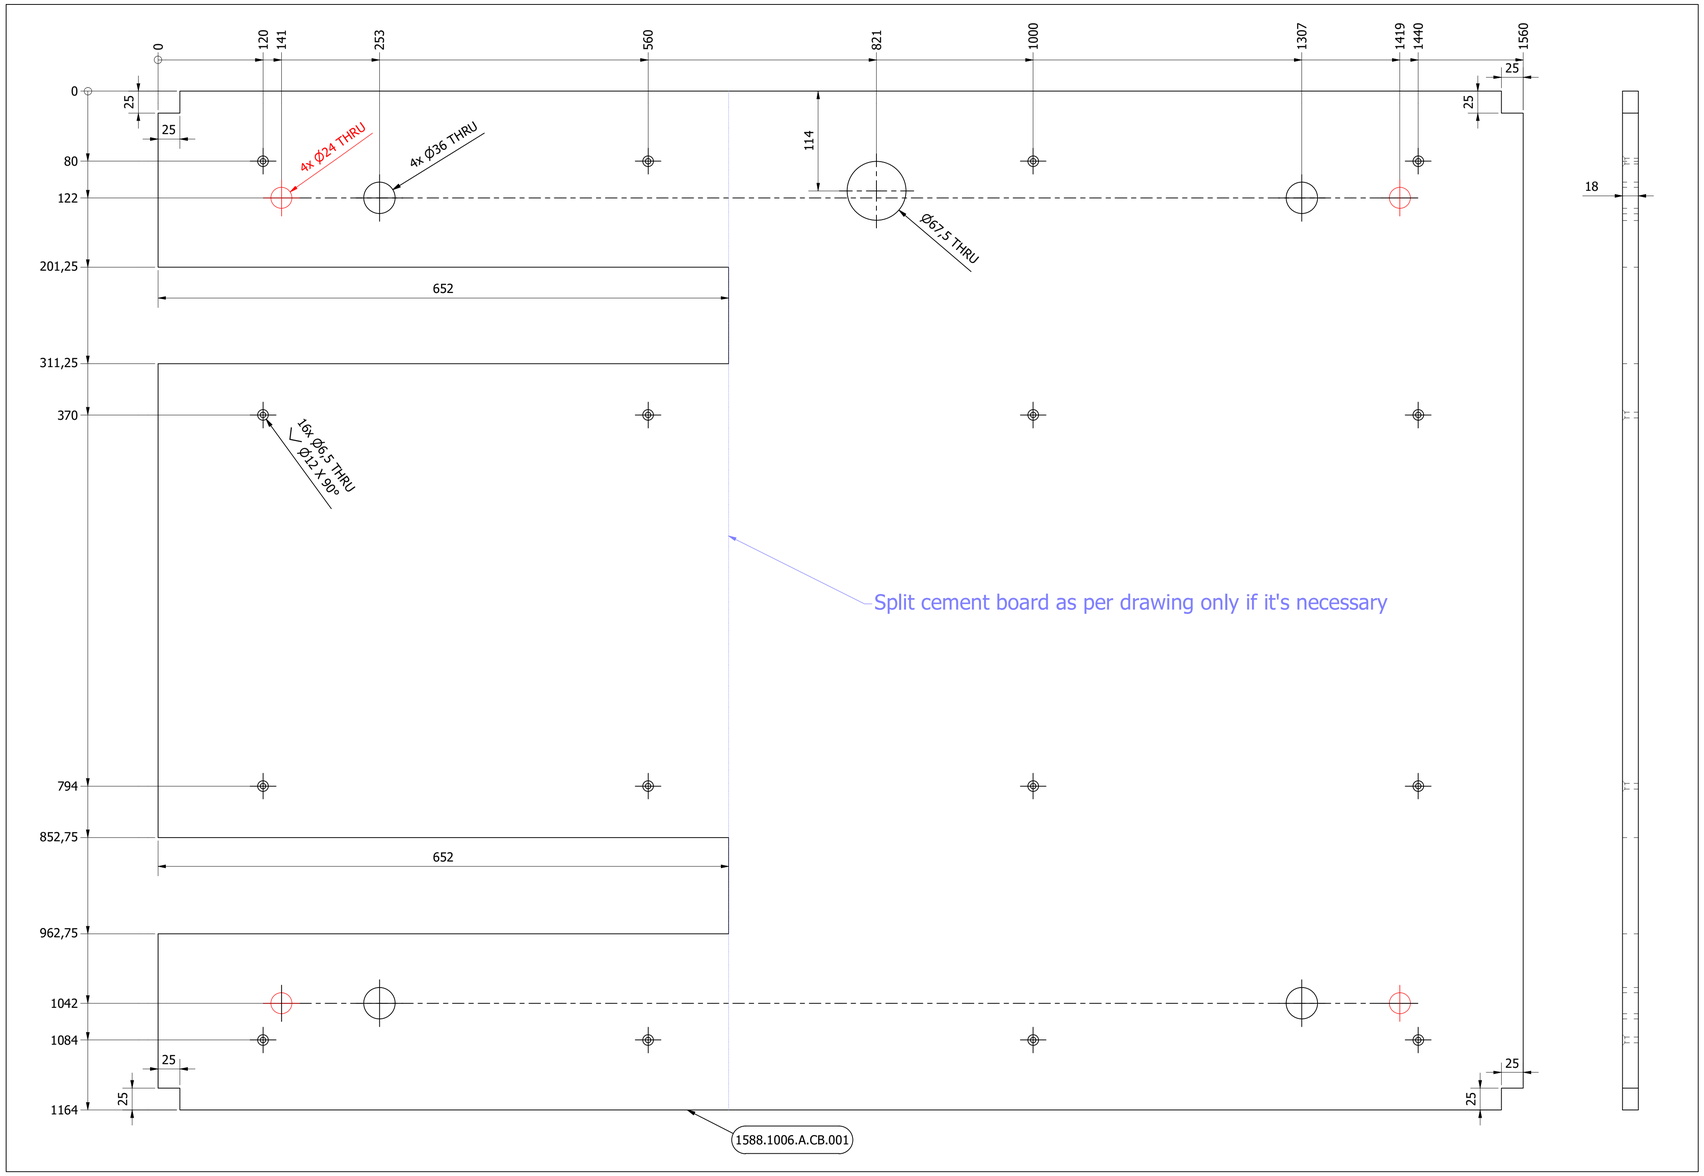

To be taken on Site 3/3

- Cement boards

This drawing and the information it contains is the property of Sesame Access Systems LTD. and must not be copied or issued to any third party

Drawn by	Checked by	Date:	Project name:	Revision
IDSPC7	S.J.Lyons	14/07/2026	1588.America Street, No.1	0

Sesame ACCESS FOR ALL
Unit 1, Cumberland Works
Wintersell Business Park
Surrey, KT14 7LF
Tel: +44 (0)1784 440088
Fax:+44 (0)870 7053252
Email:forall@sesameaccess.com
Web:www.sesameaccess.com

Drawing pack: 1588.America Street, No.1_EngineeringDrawing.dwg

Process type: C - cutting, W - Welding, A - Assembly

Sheet 12 / 12